



ECOLE MÂNTULEASA

ATELIER COMMUN-E - ZEINEB AZZAOUI - YASMINE BEN GUIRAT

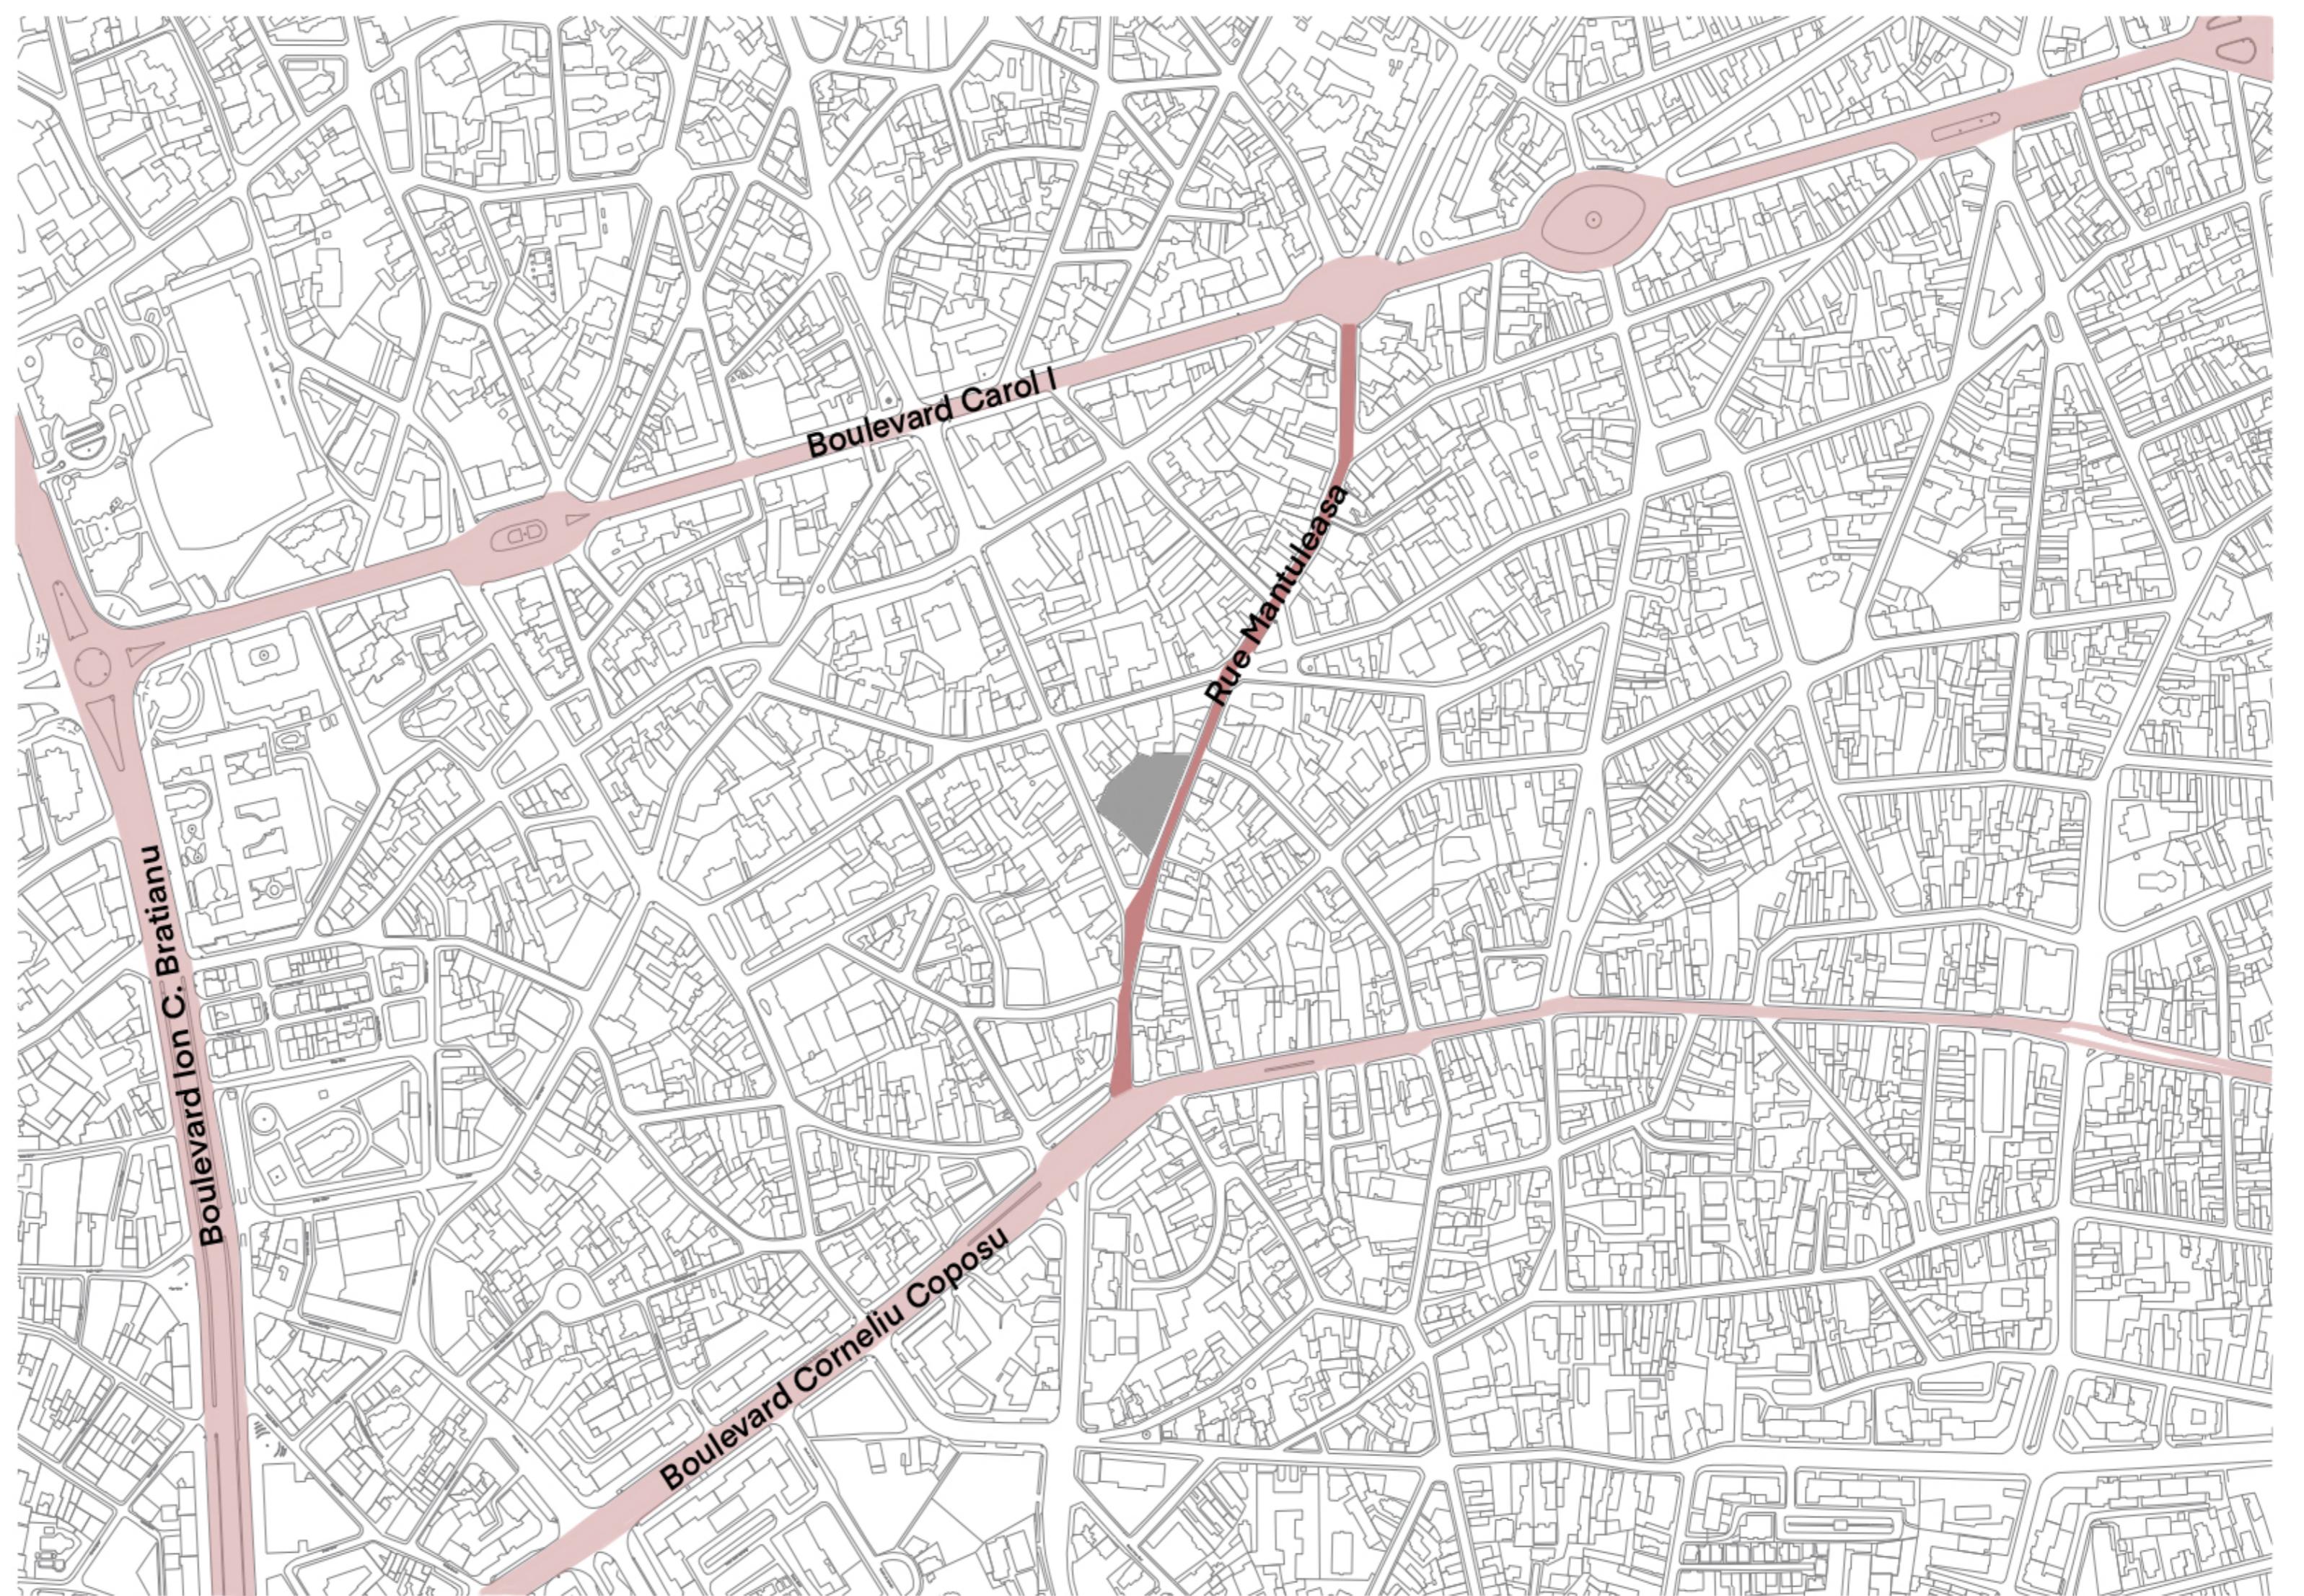

AFFECTATIONS LIÉES À L'ENFANCE

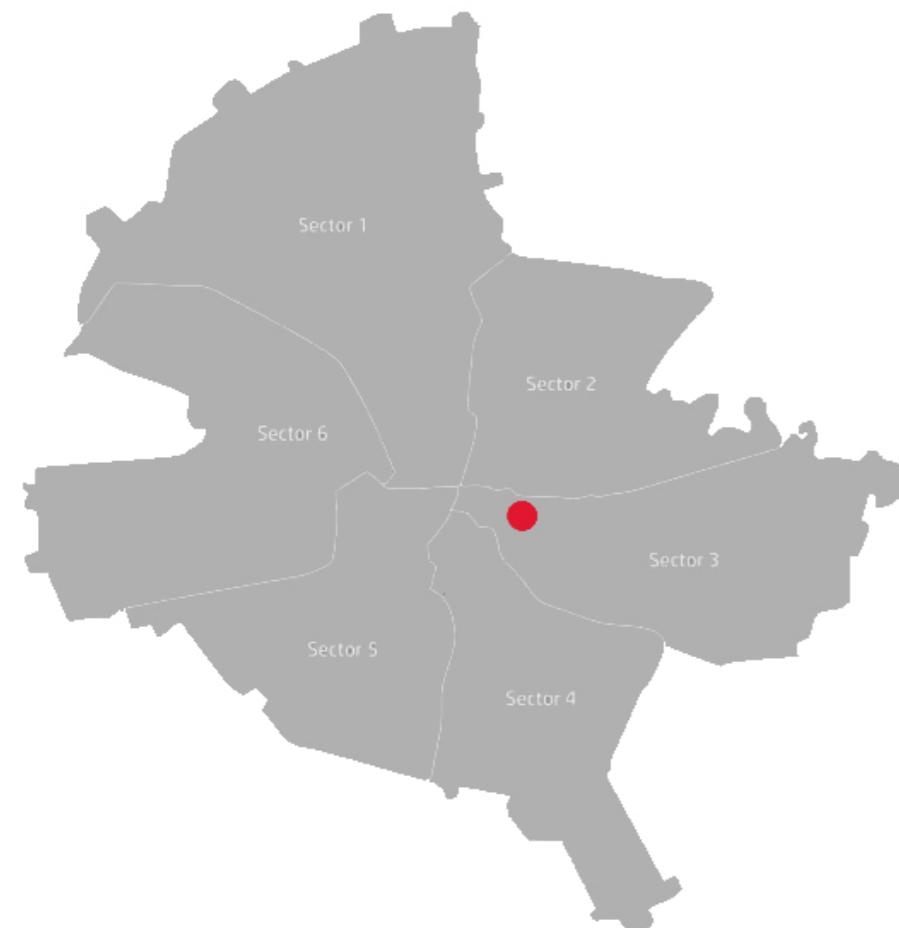

AFFECTATIONS DU QUARTIER



NATURE DES ESPACES




POROSITÉ DES ÎLOTS



RÉGIME DES HAUTEURS



FLUX DE CIRCULATION

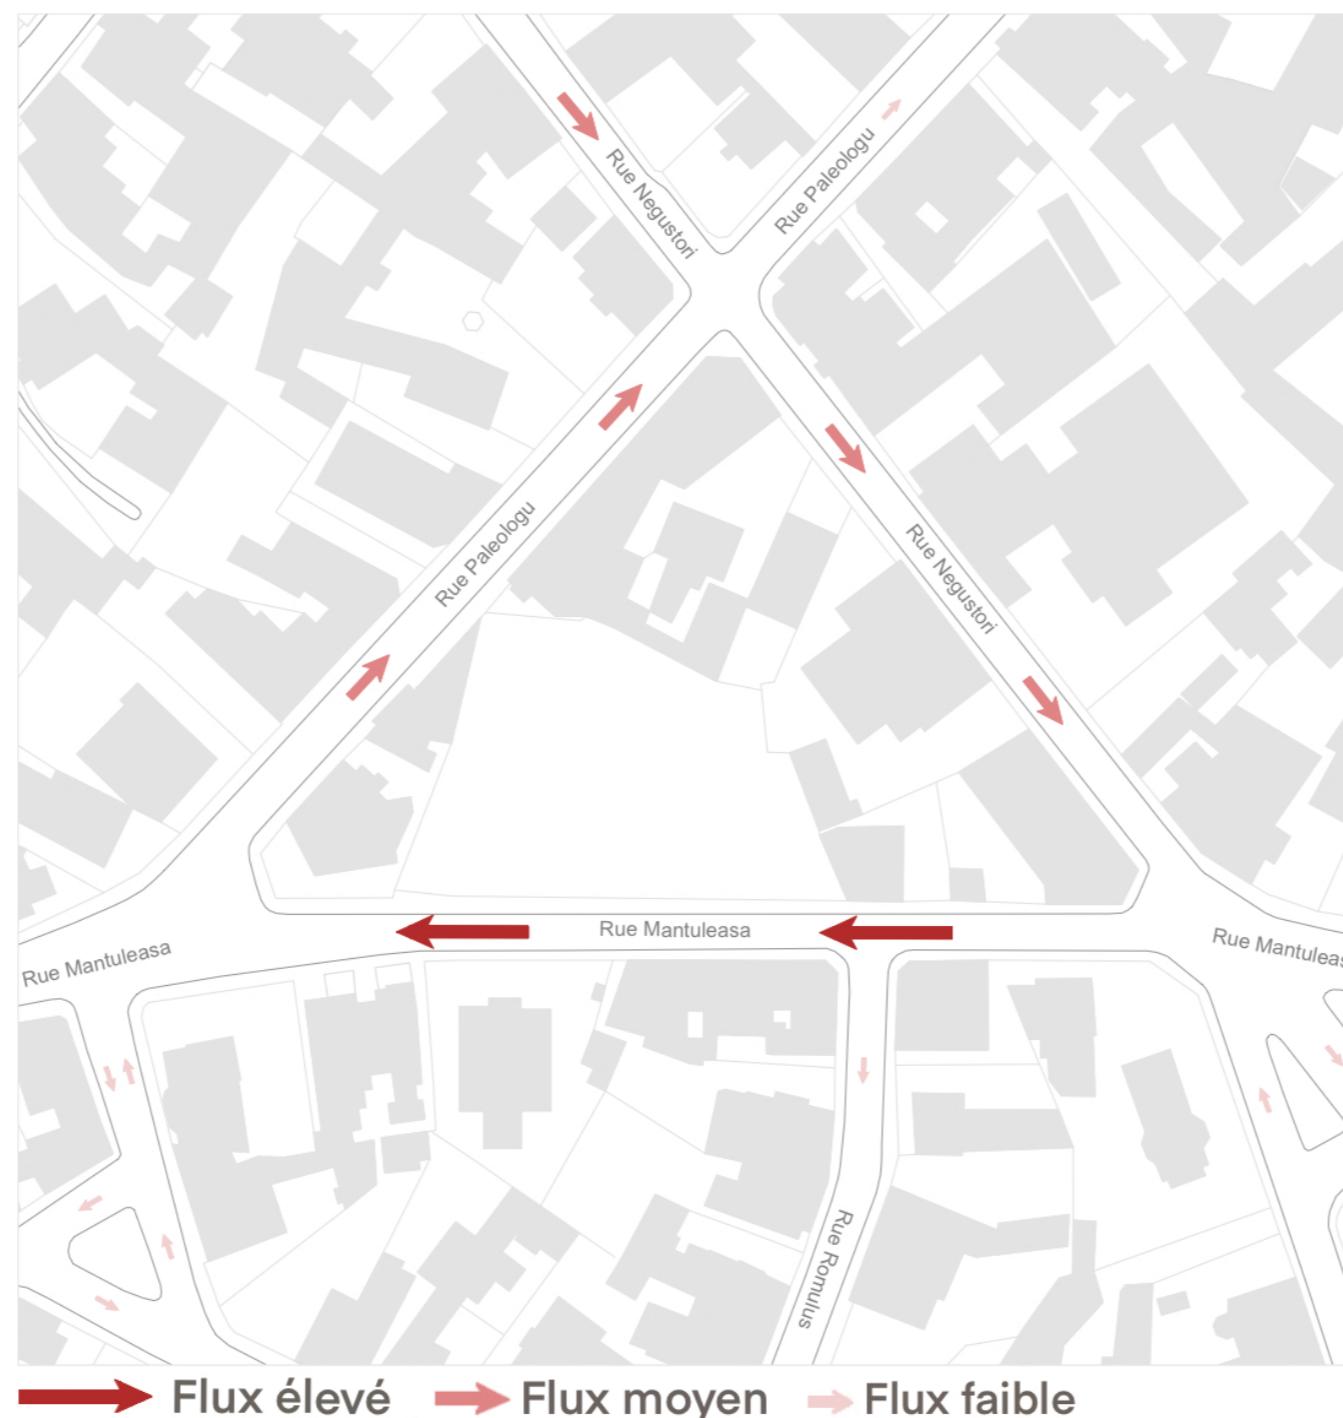


VÉGÉTATION PRÉSENTE




HAUTEURS & MATÉRIALITÉ DU VOISINAGE




DIMENSIONS DE LA PARCELLE

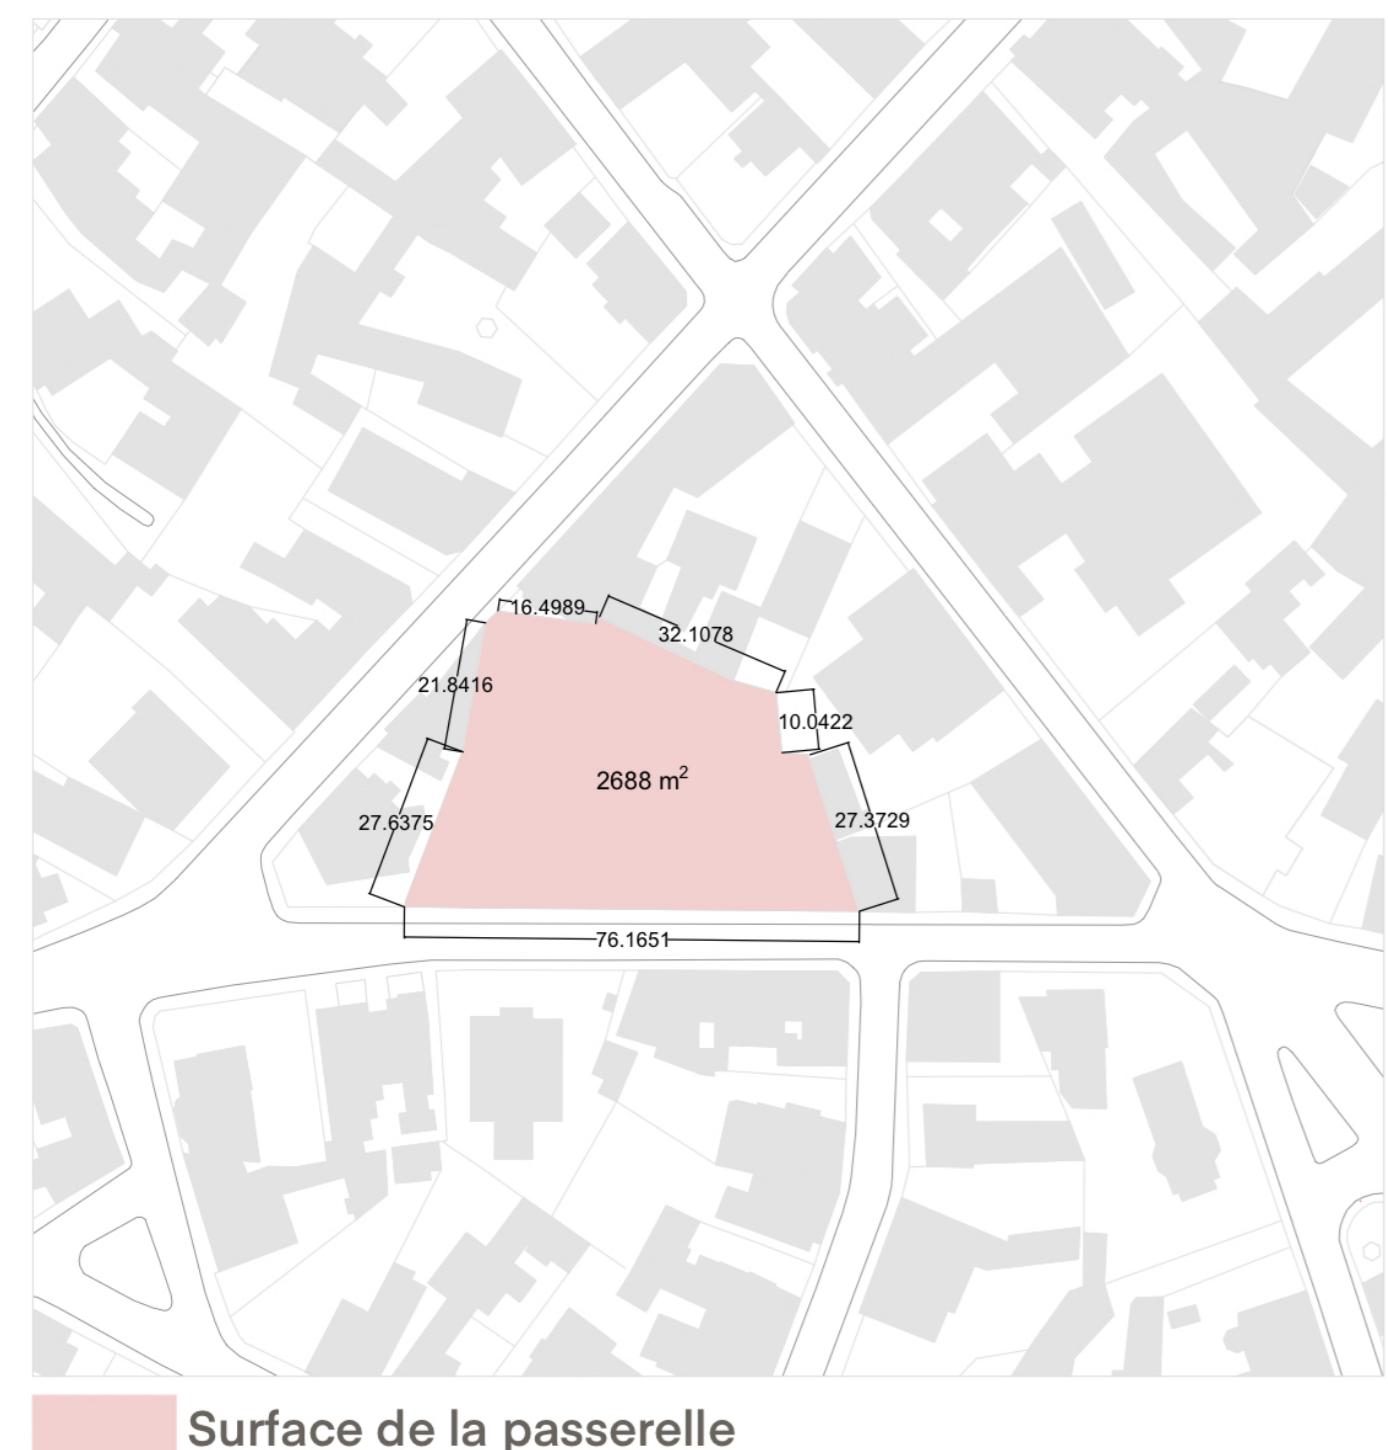

RÉGLEMENTATIONS PUZ

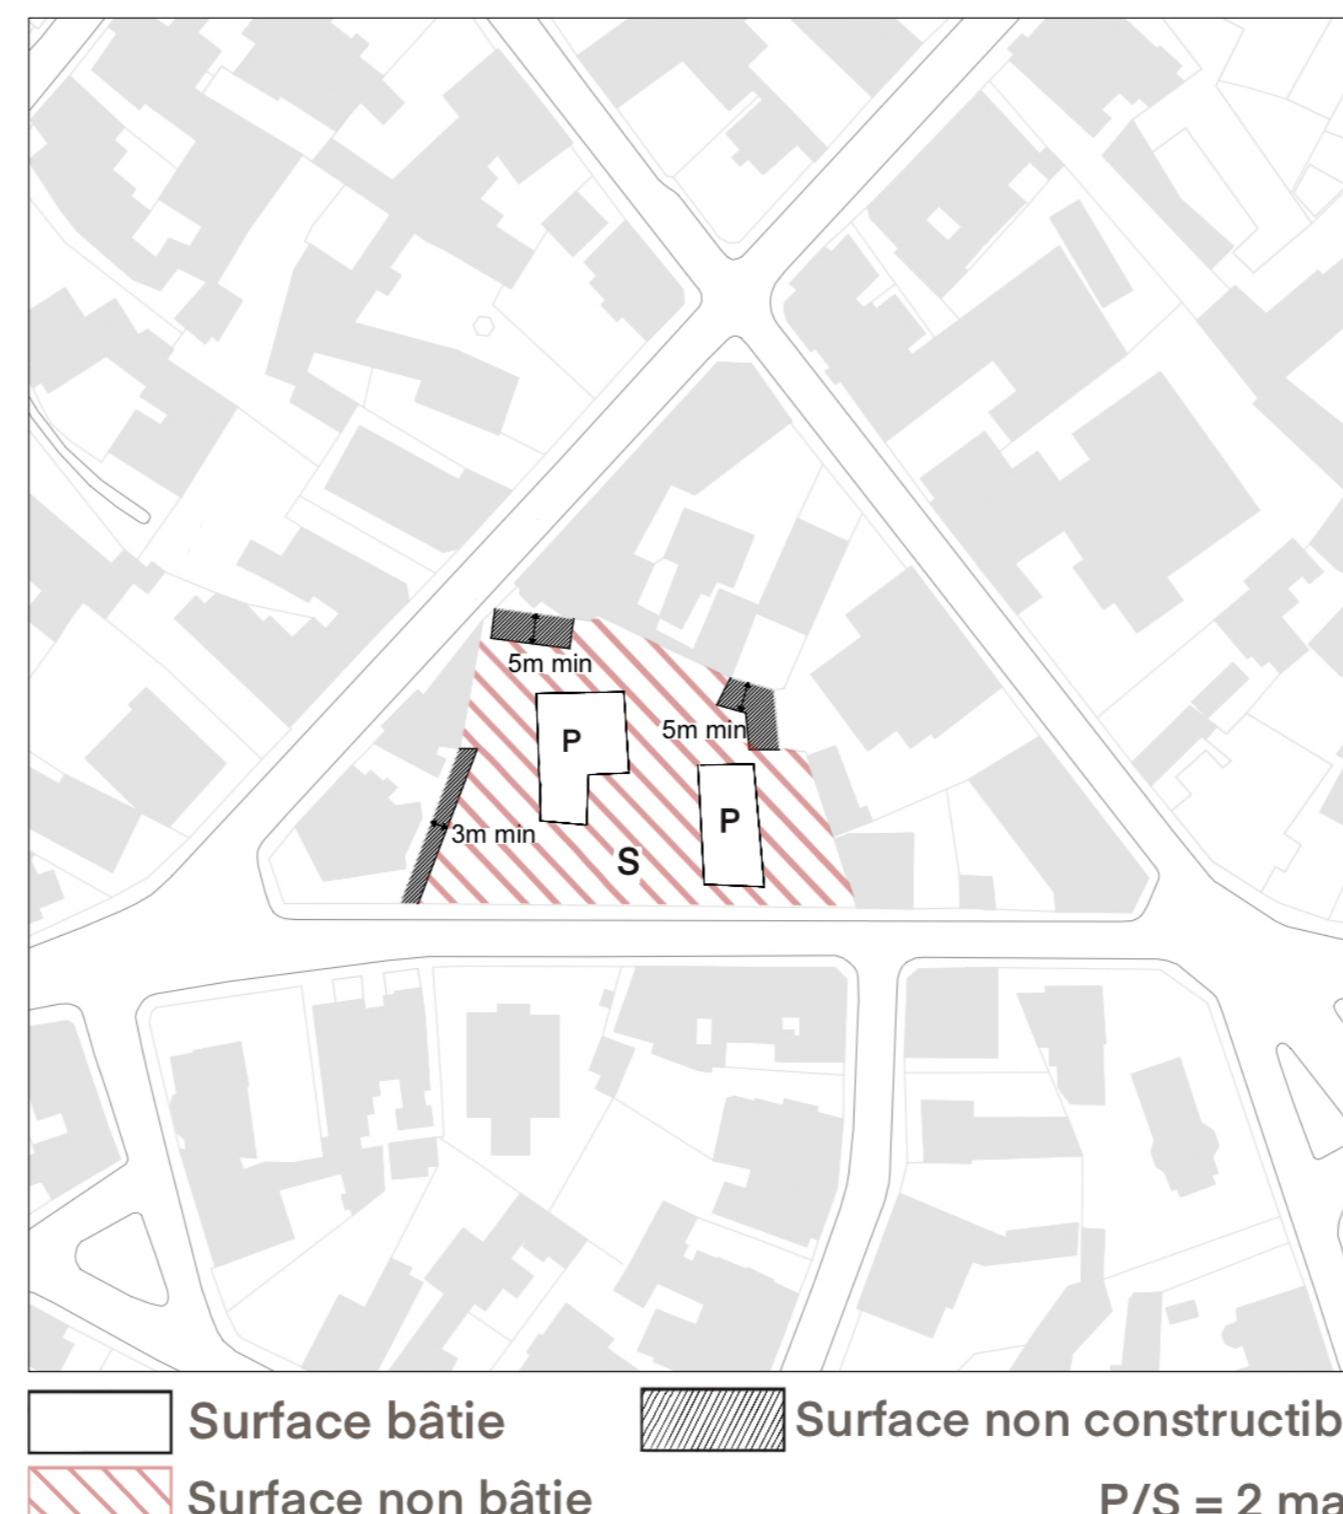

ACCÈS AU SITE

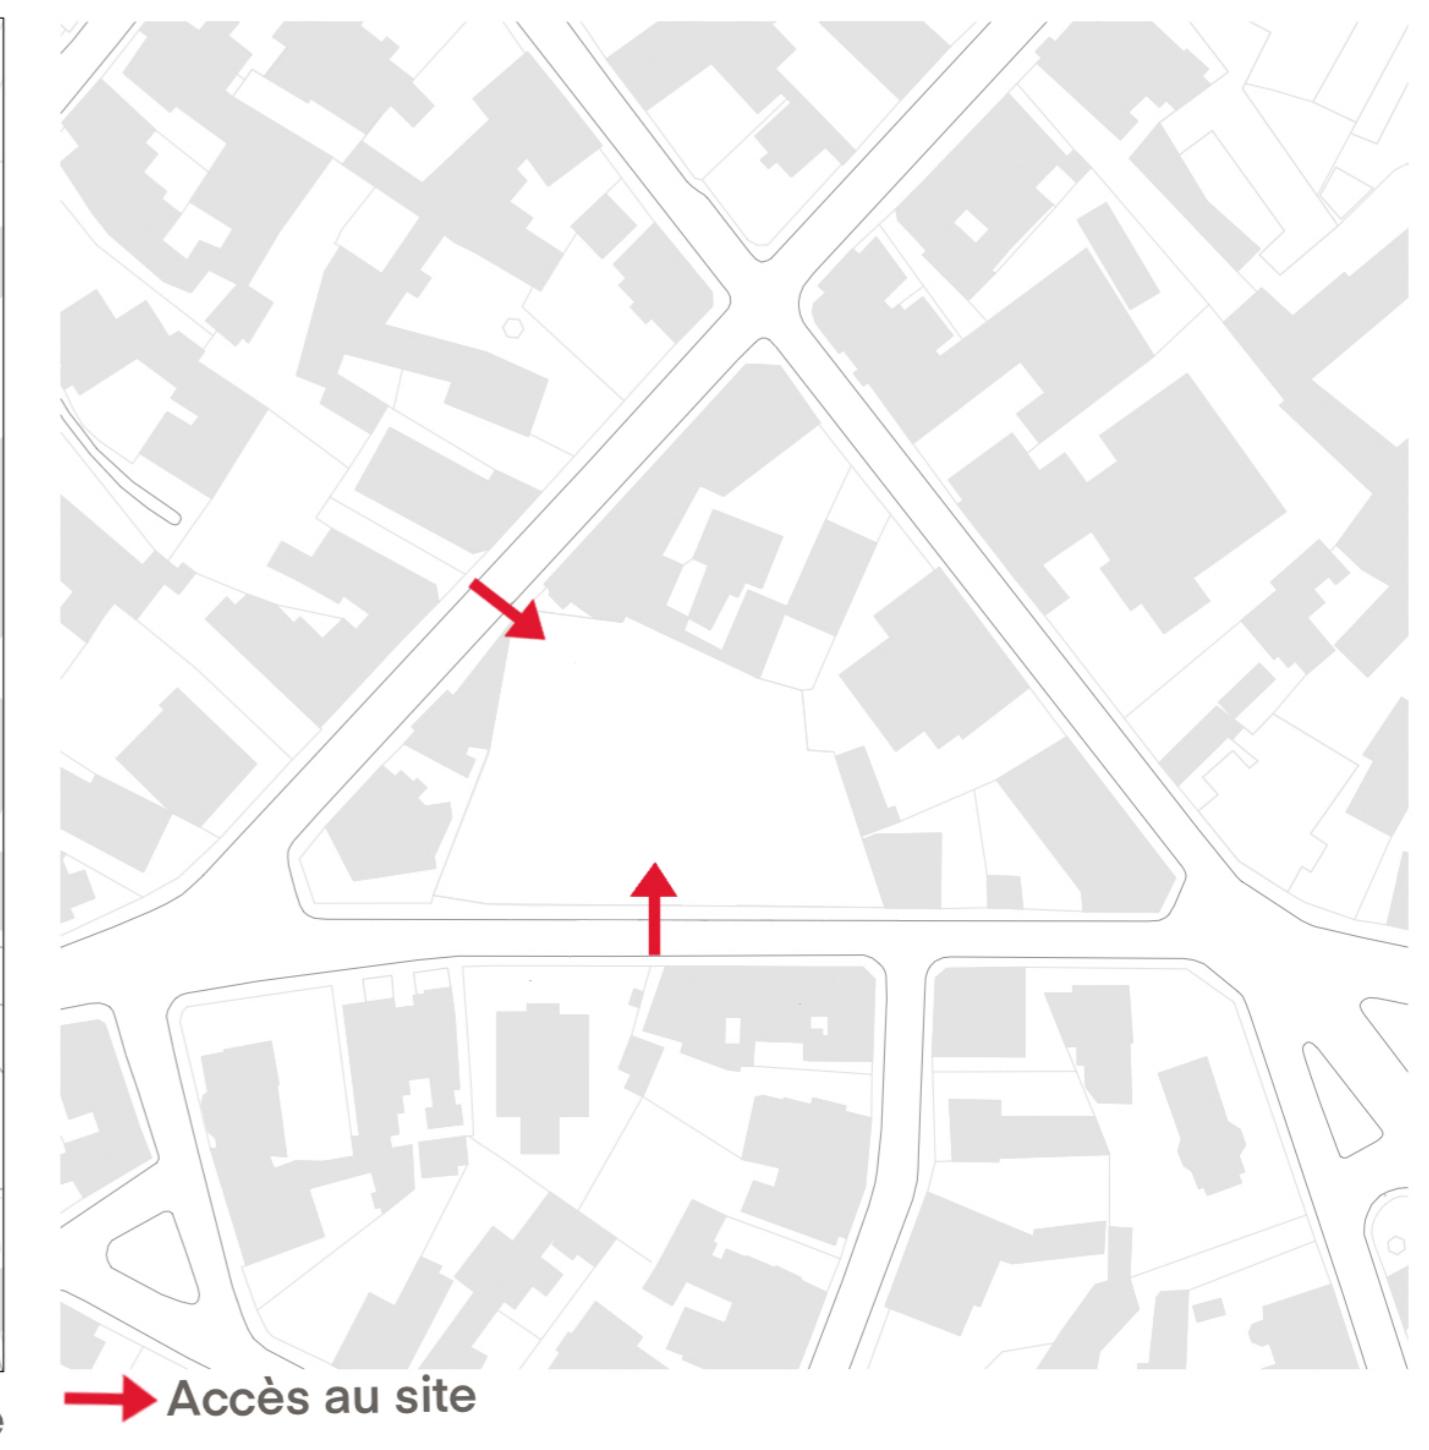

FACADES EXPLOITABLES DU SITE




TROTTOIRS NON ADAPTÉS



INTENTIONS


DIMINUER LA PART AUTOMOBILE

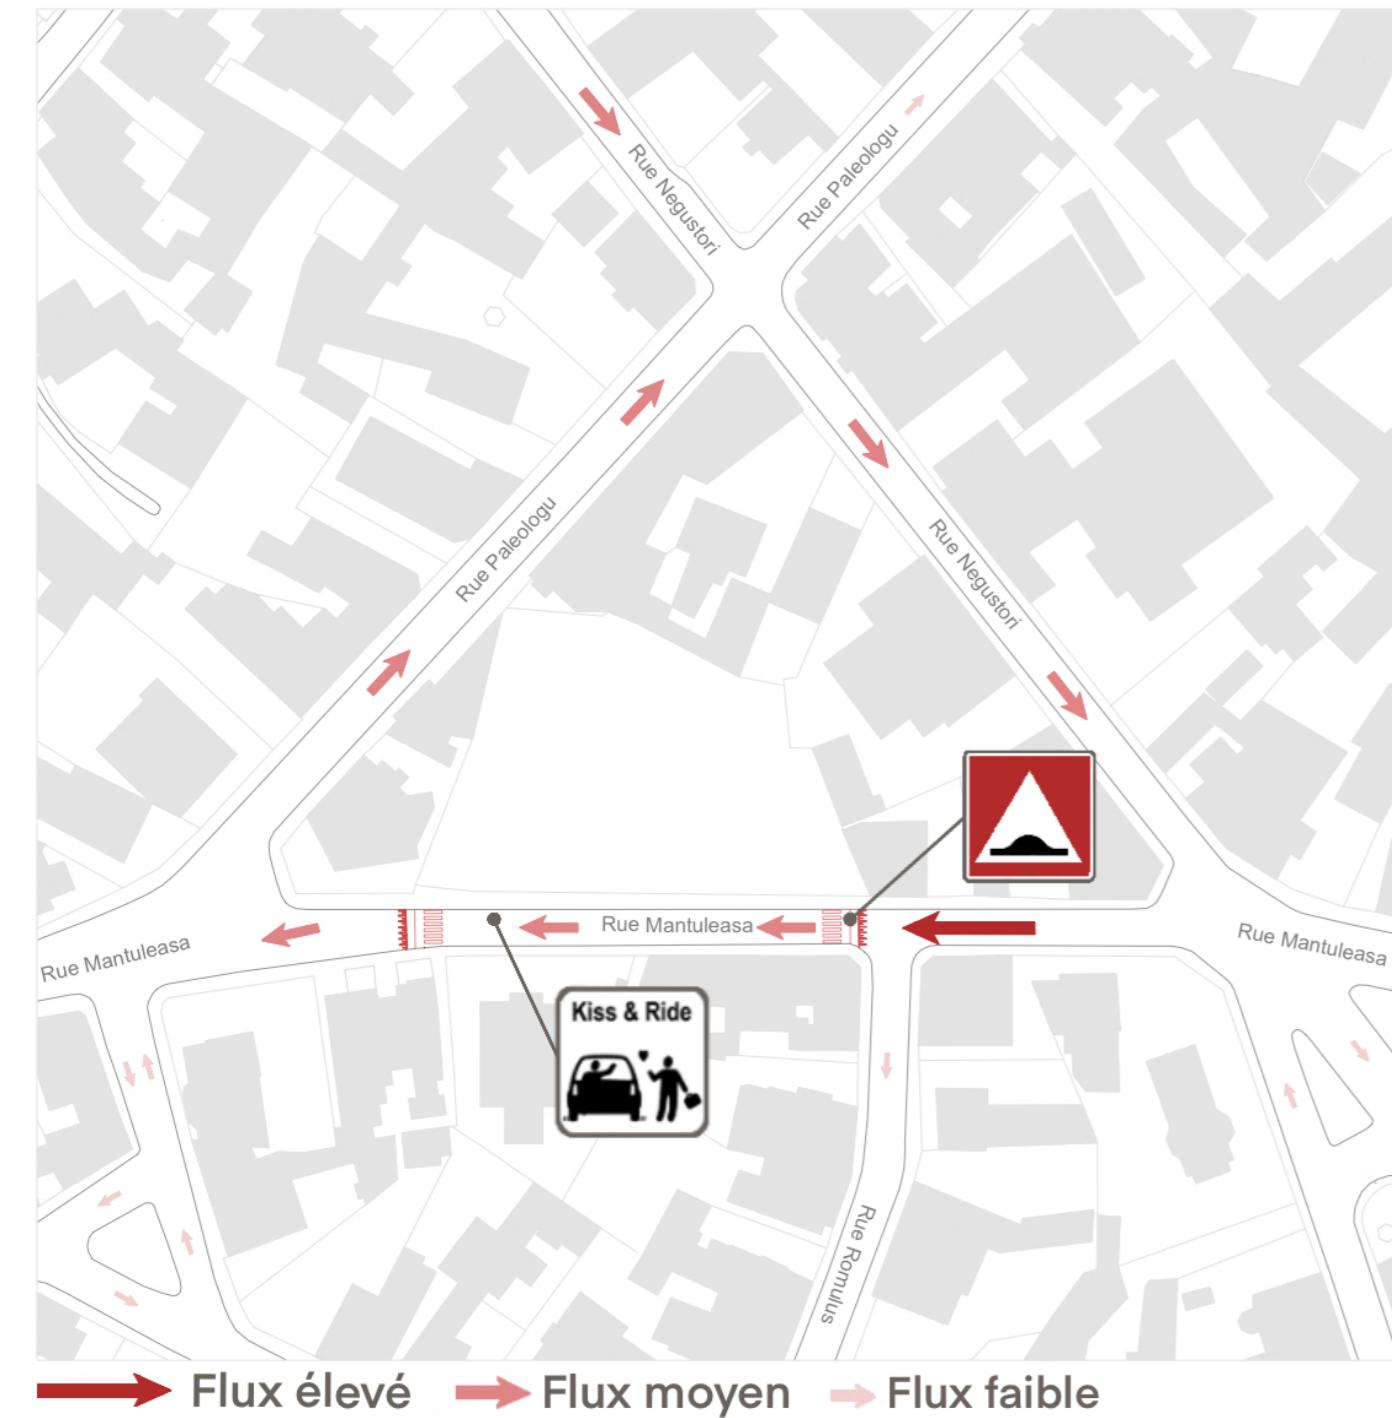


EXPLOITATION DES MITOYENS



RESPECT DES NORMES PUZ

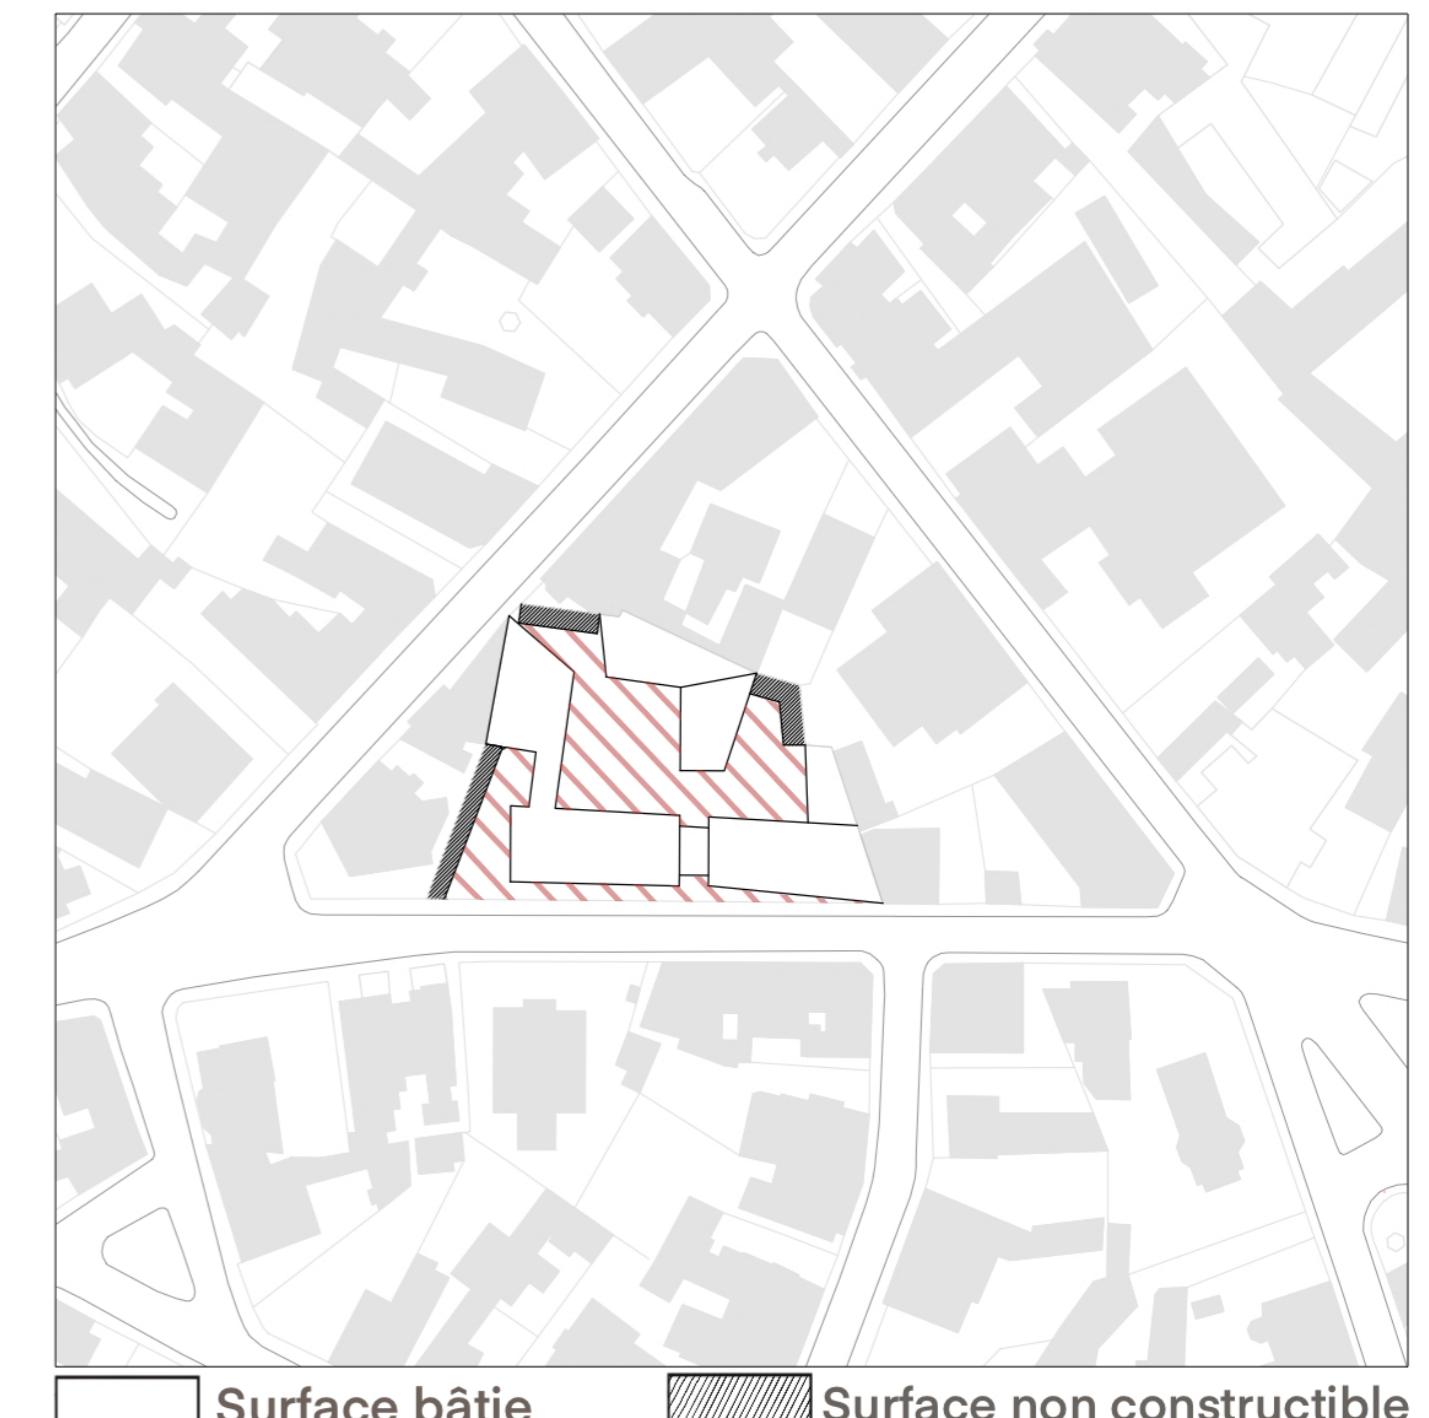


ACCÉSIBILITÉ

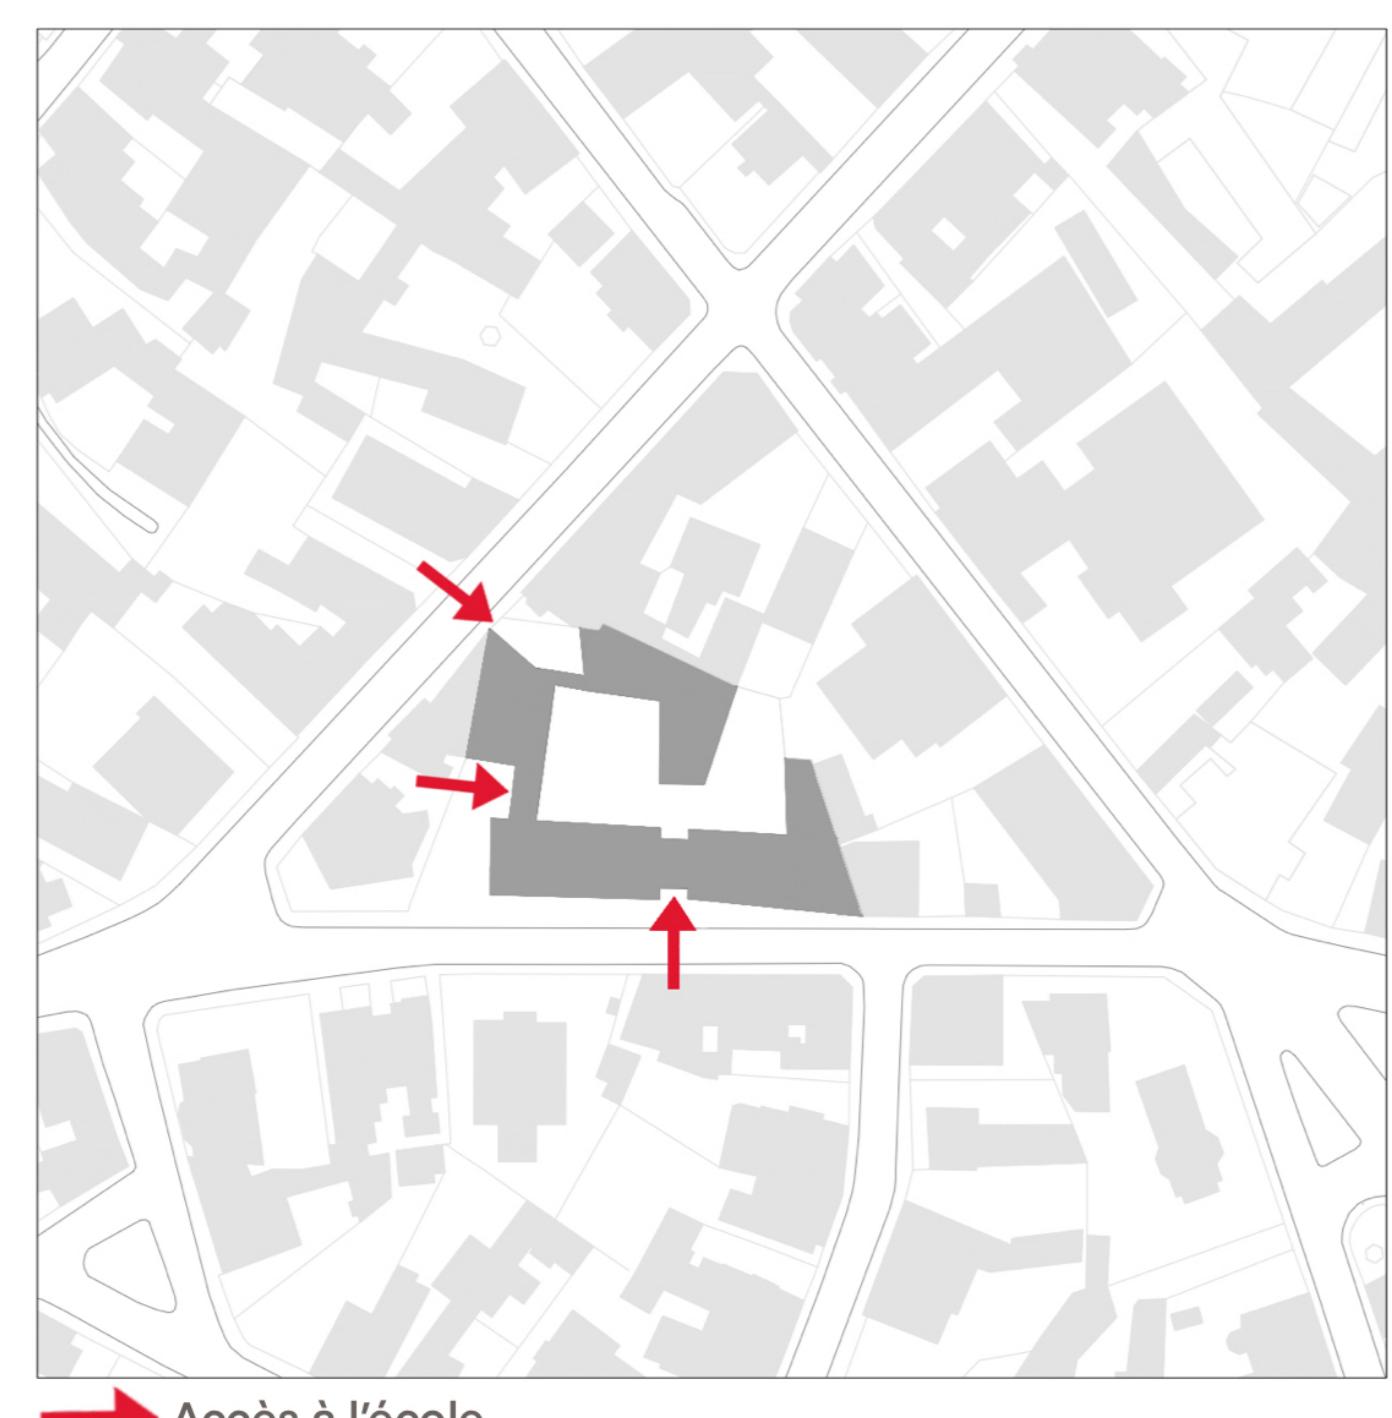


COURS ADAPTÉES A L'ENFANT




Évoquer les questions de communauté (cohésion, partage..) et d'ouverture (porosité, partage)

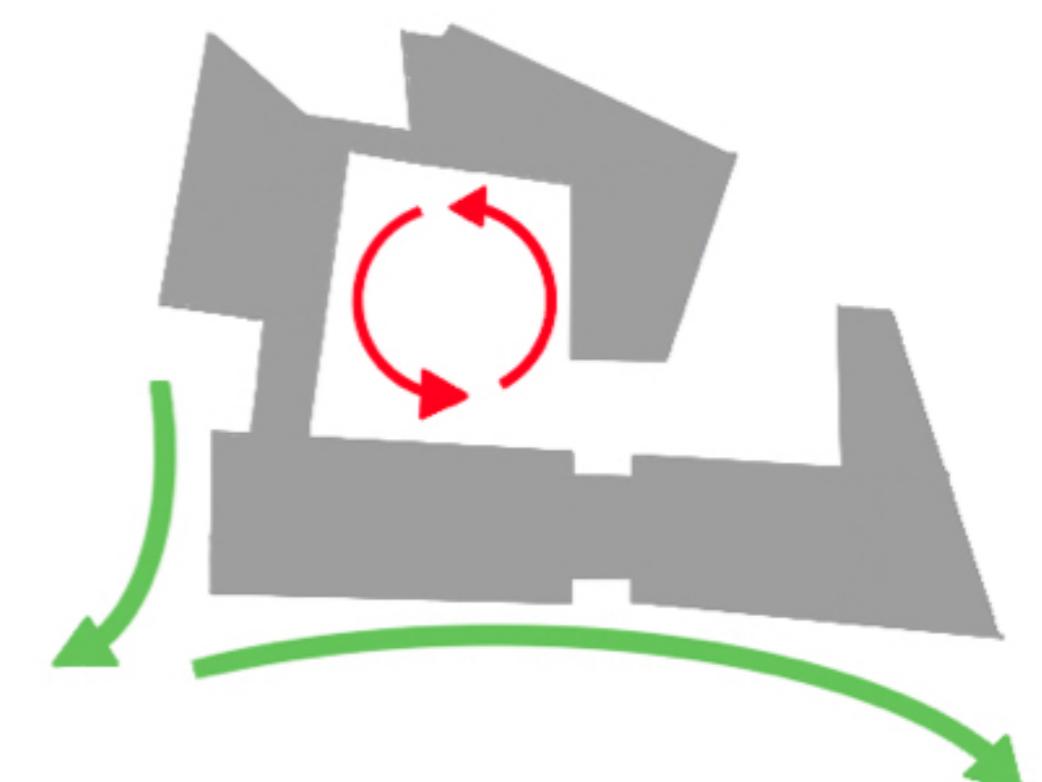


INTÉGRATION AU CONTEXTE

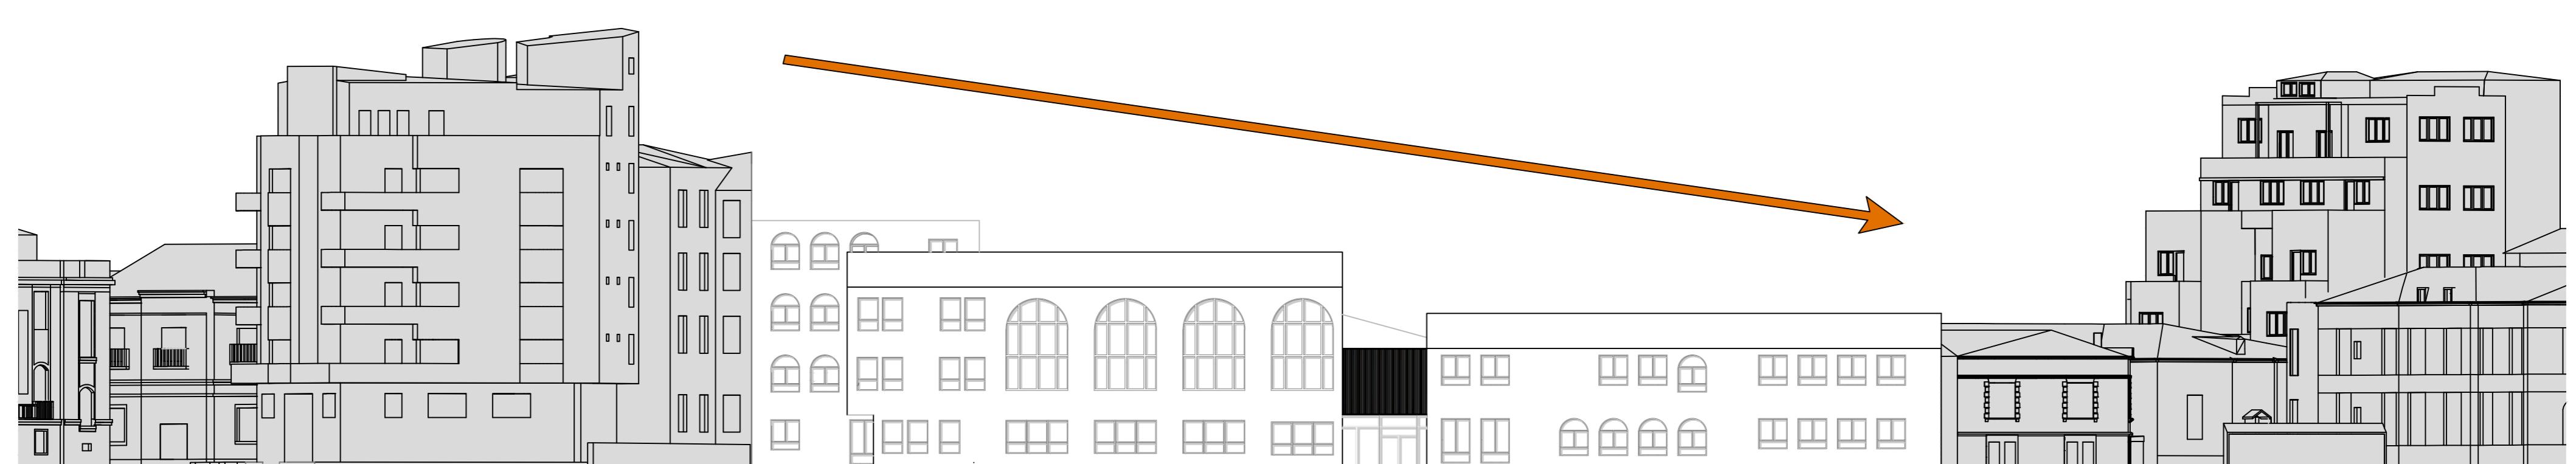

PROGRAMME

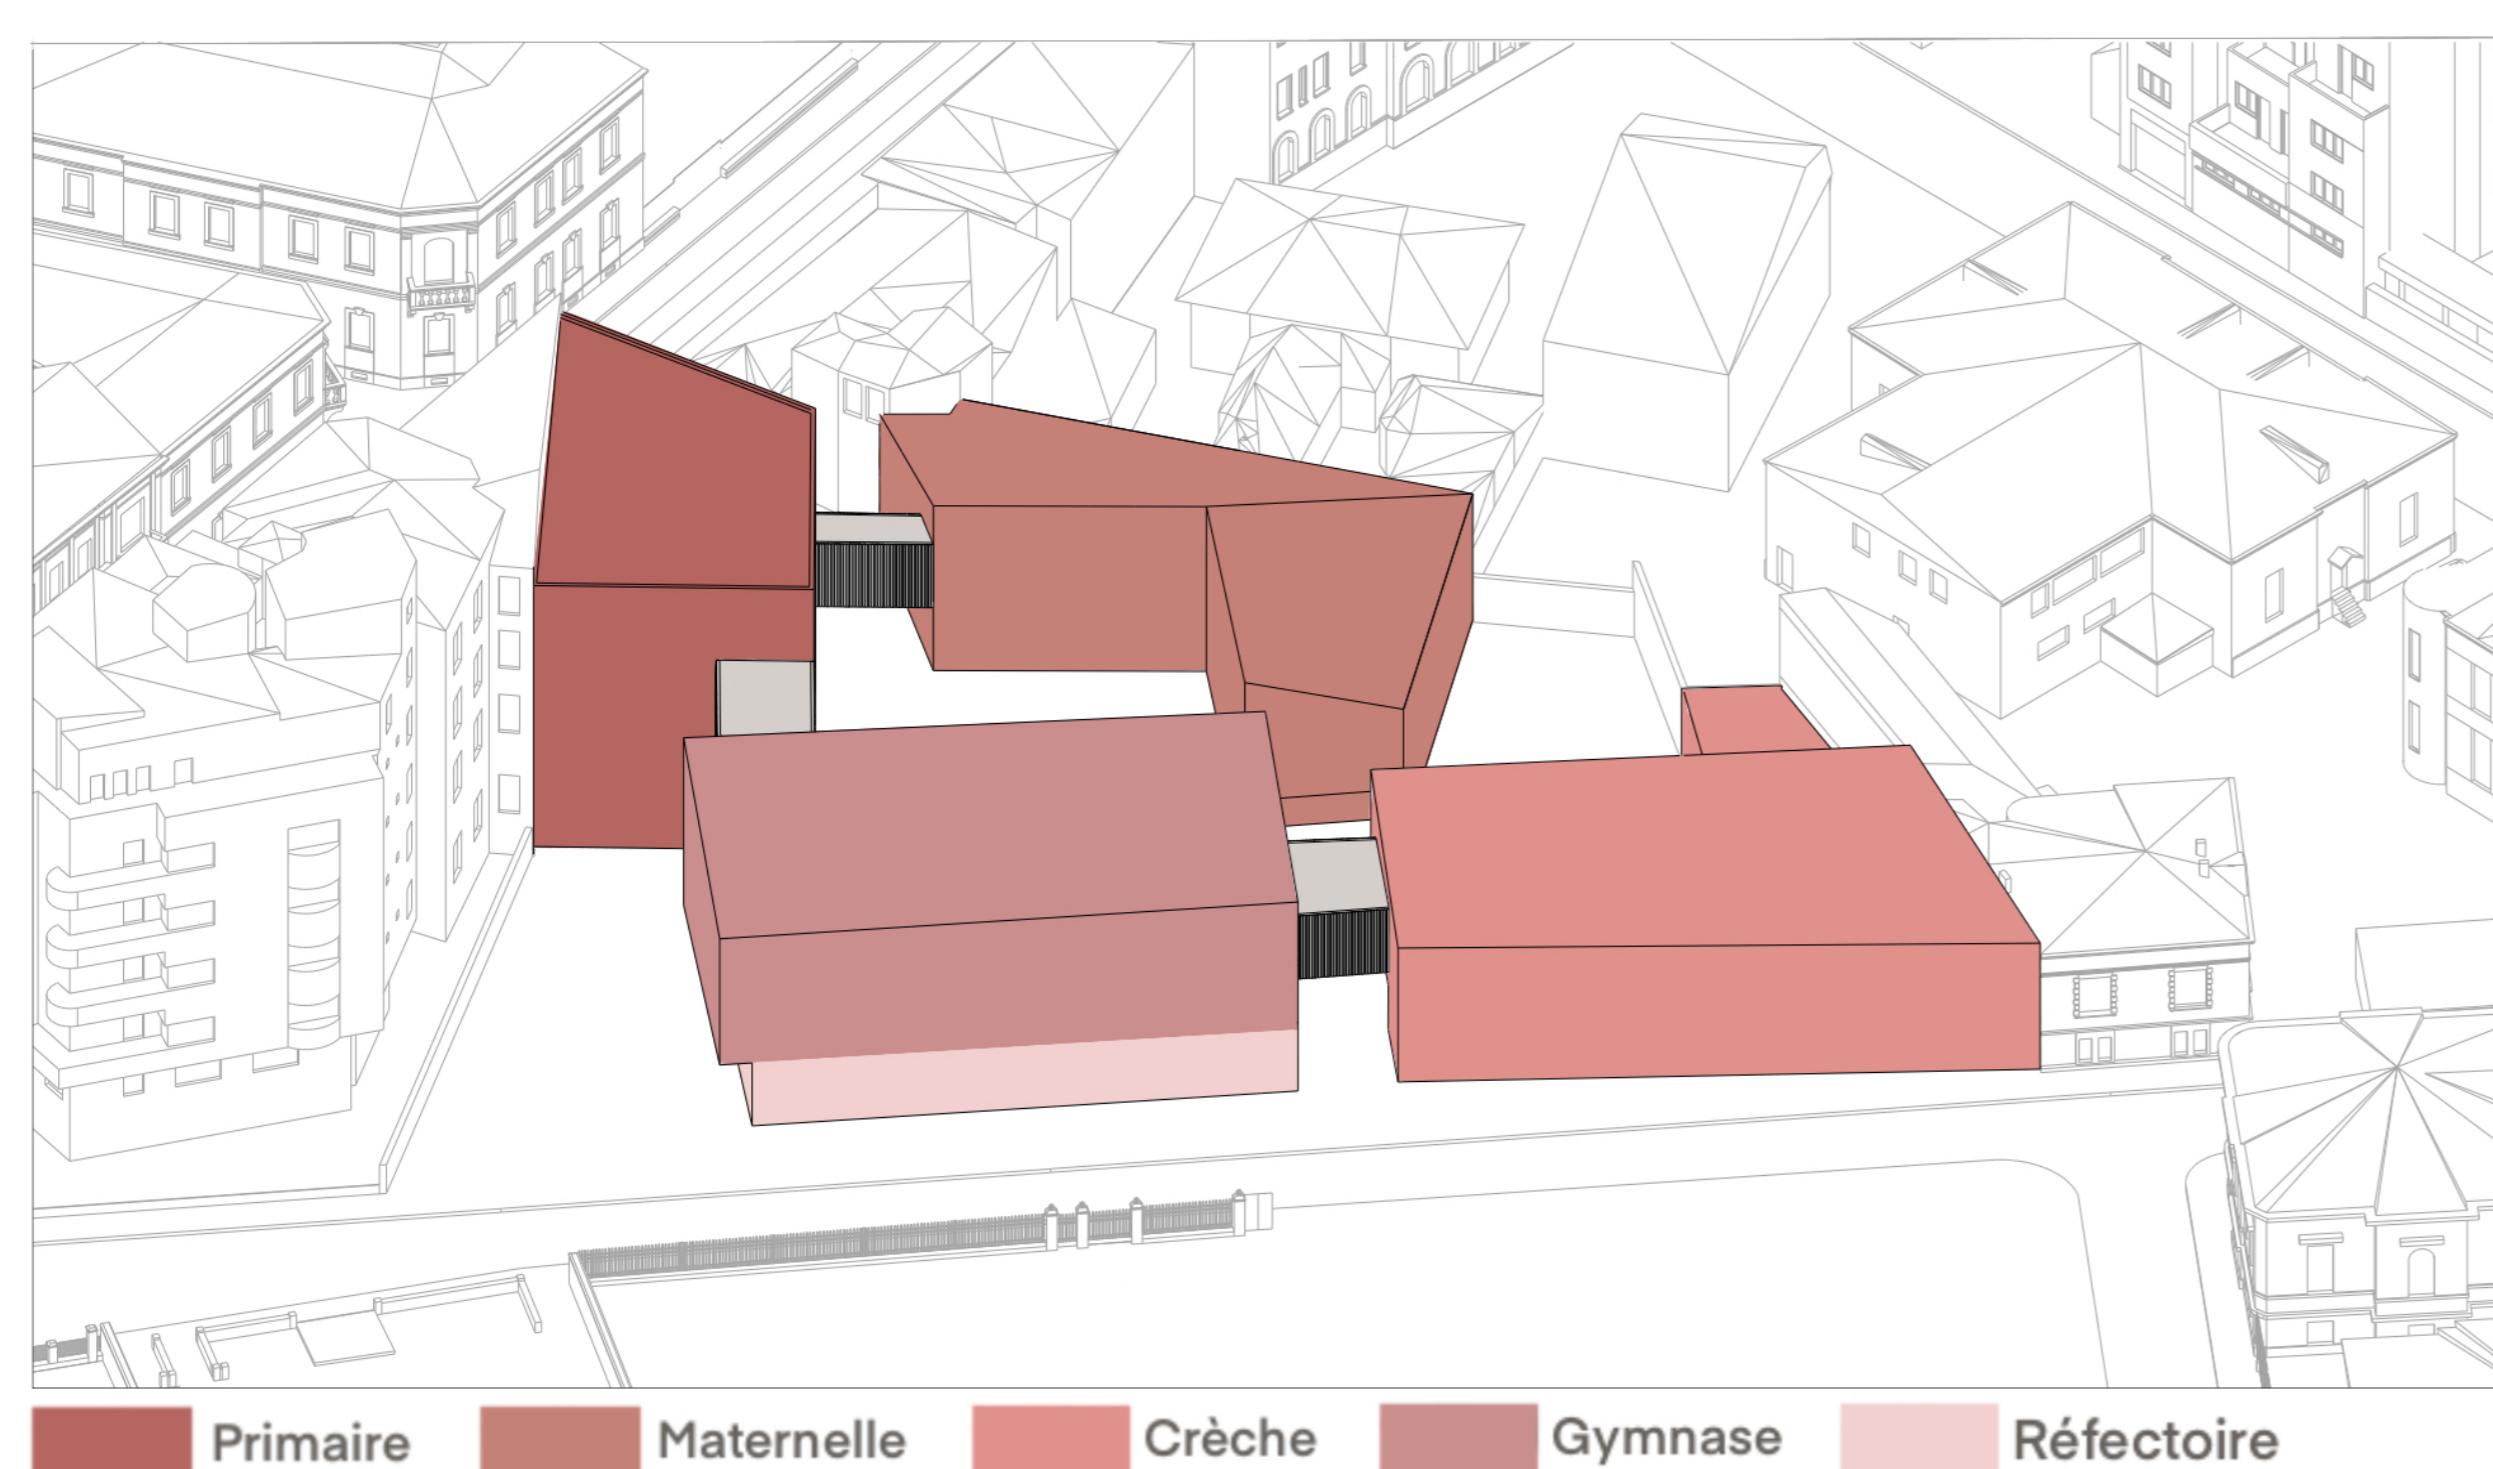


CRÉATION D'UN ESPACE DE RENCONTRE

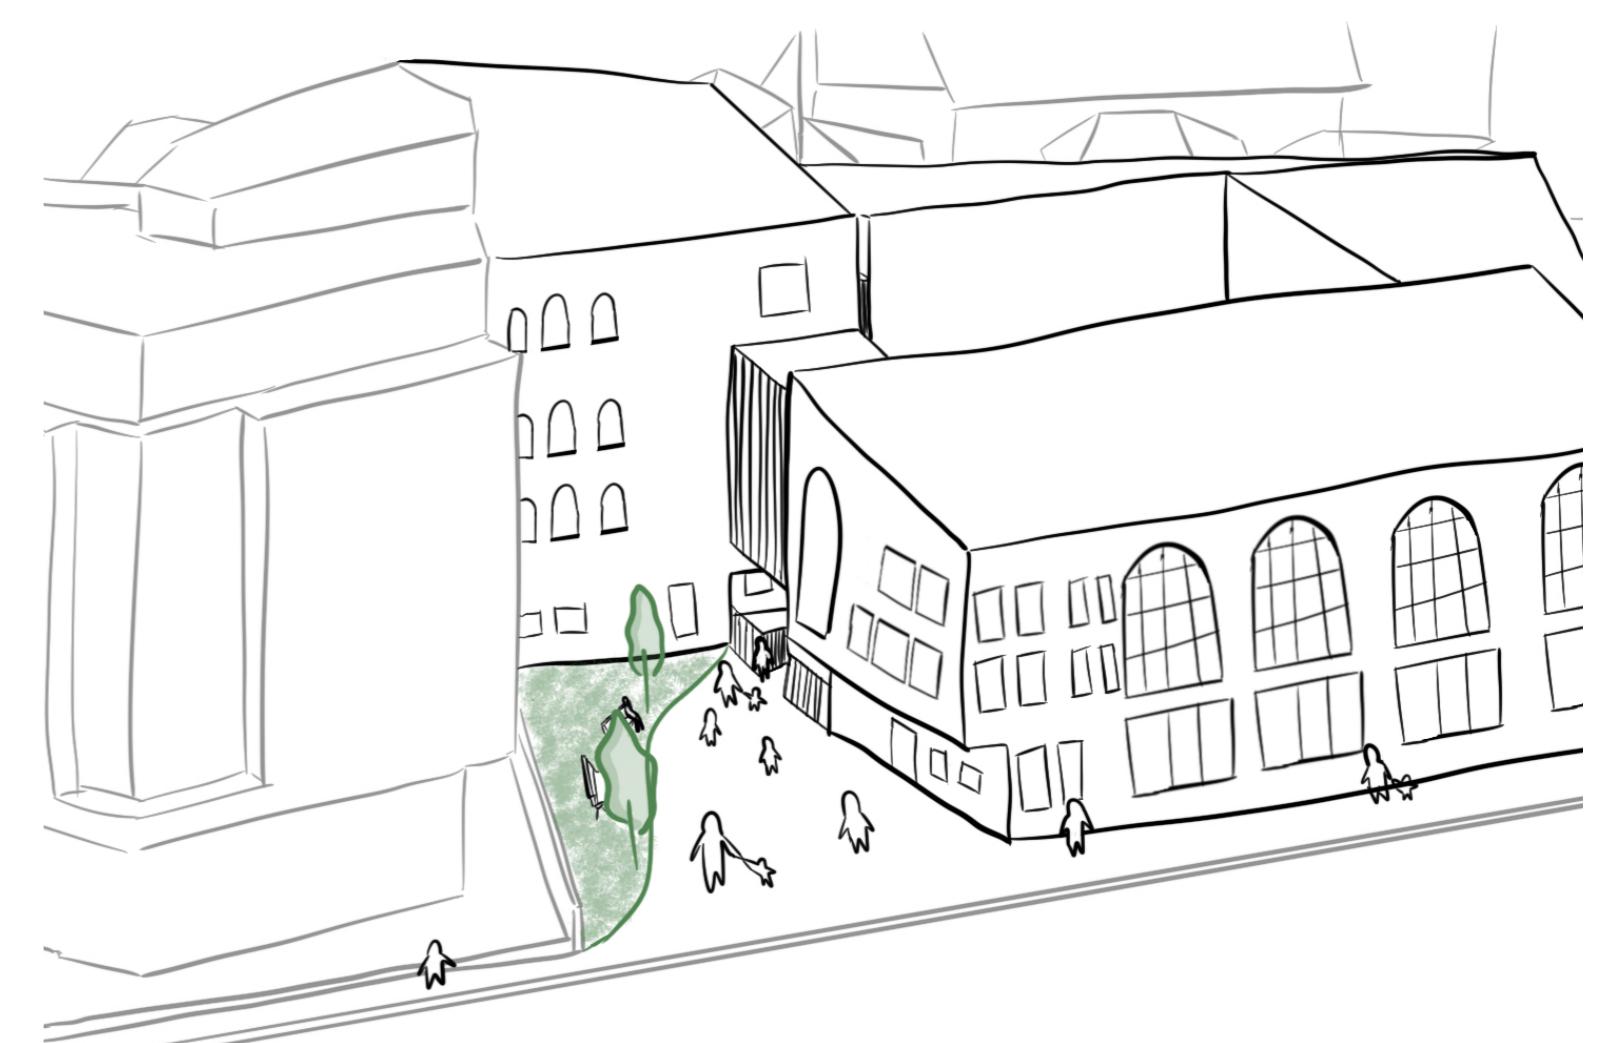


MUTUALISATION DES ESPACES


UNE SALLE DE GYM

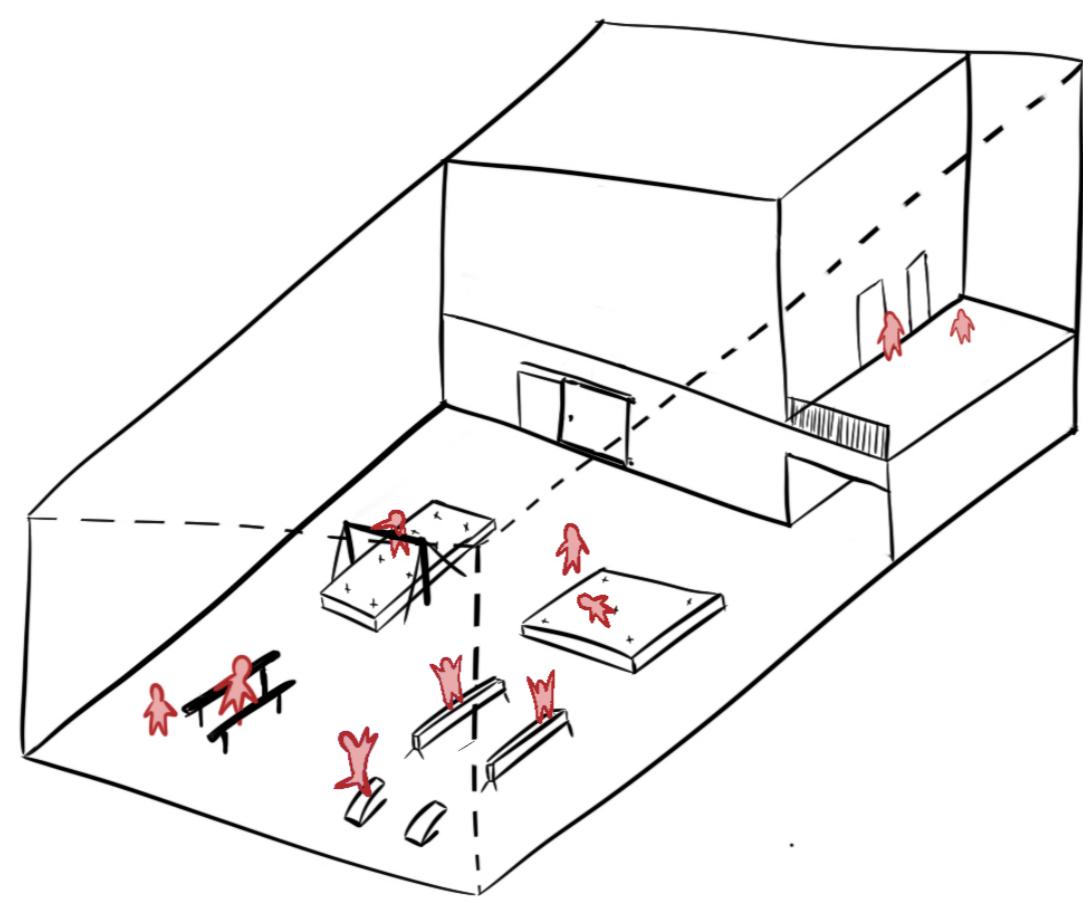


QUI PEUT DEVENIR

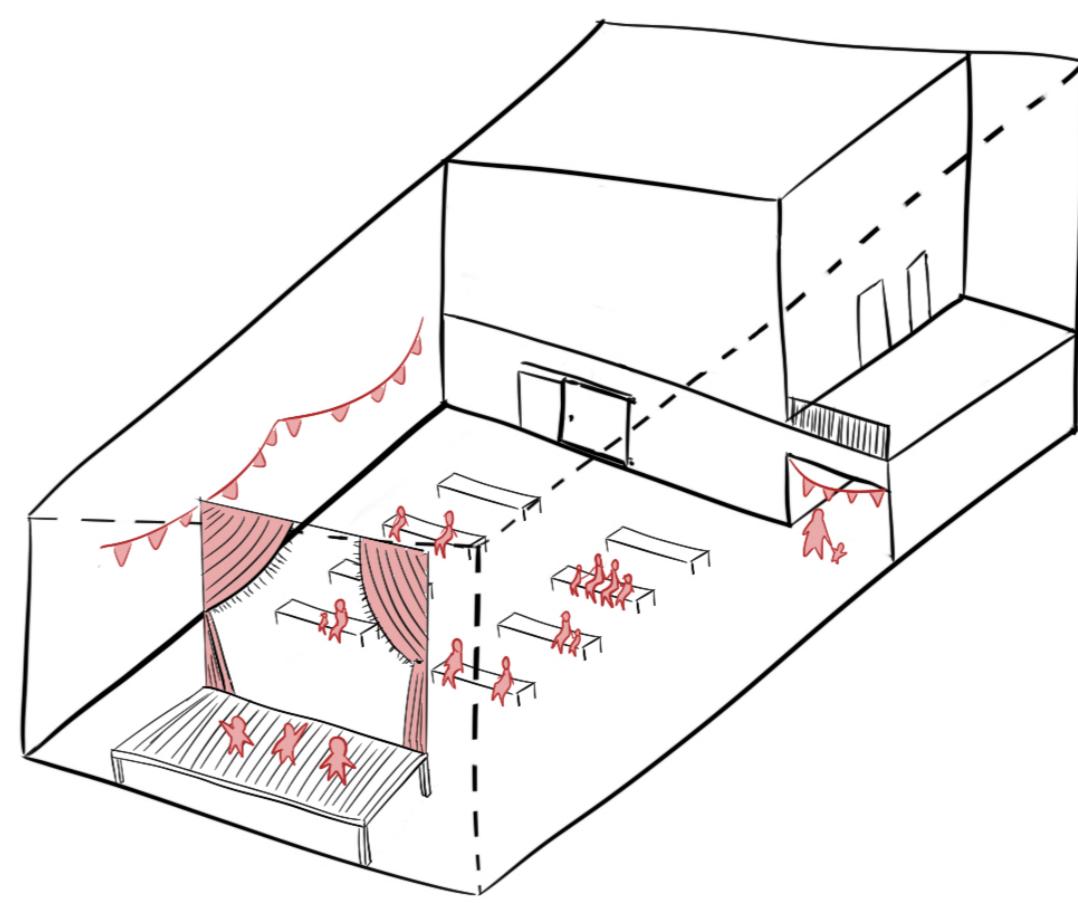


UN LARGE COULOIR

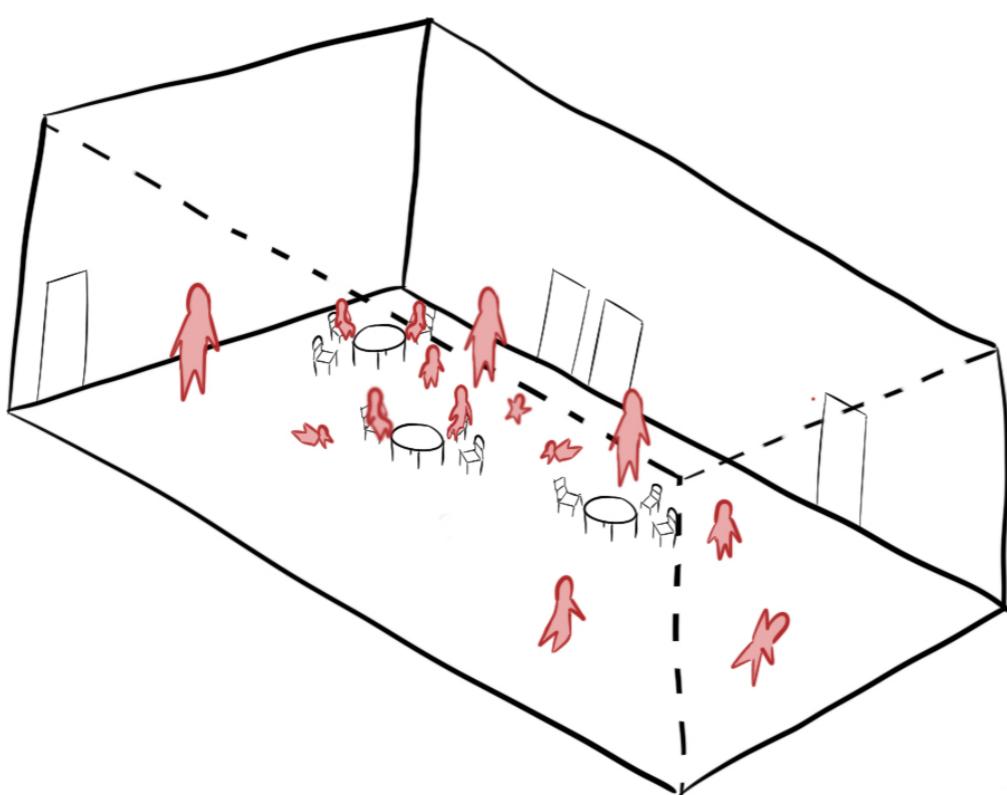


QUI PEUT DEVENIR

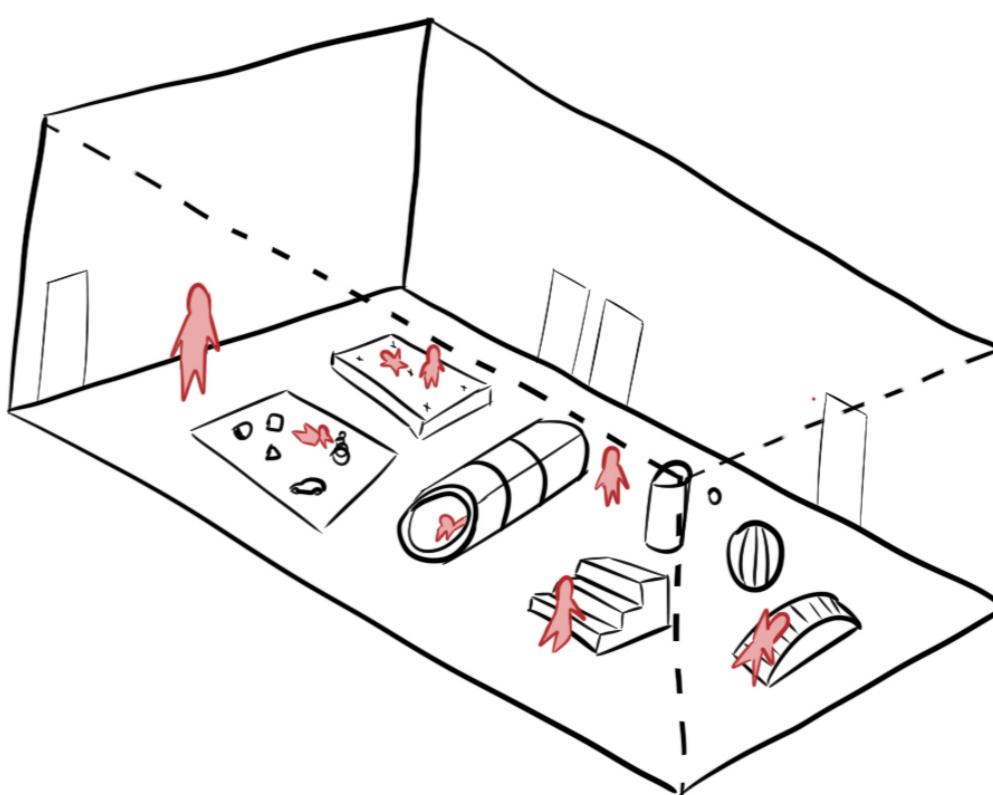

UN ATELIER DE PEINTURE

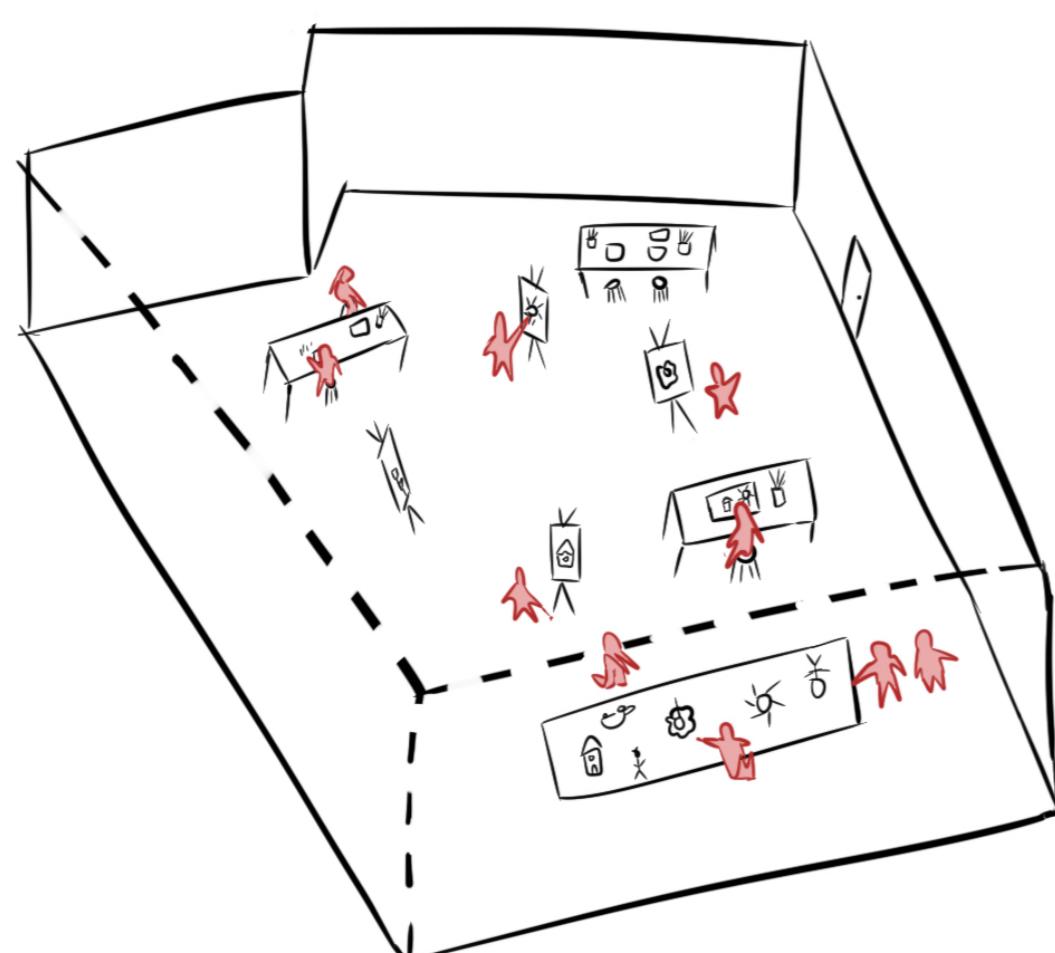


QUI PEUT DEVENIR

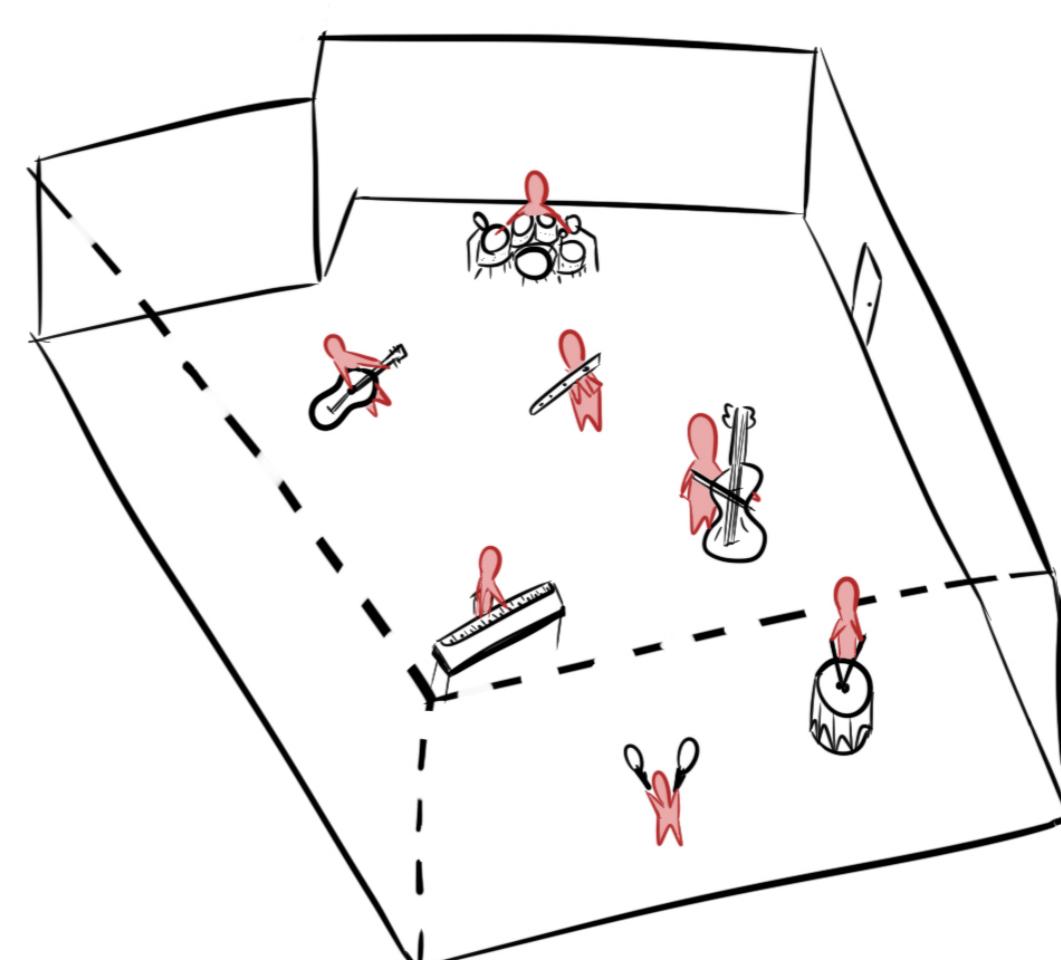


UNE SALLE DE MUSIQUE

OMNIPRÉSENCE DU COMMUN

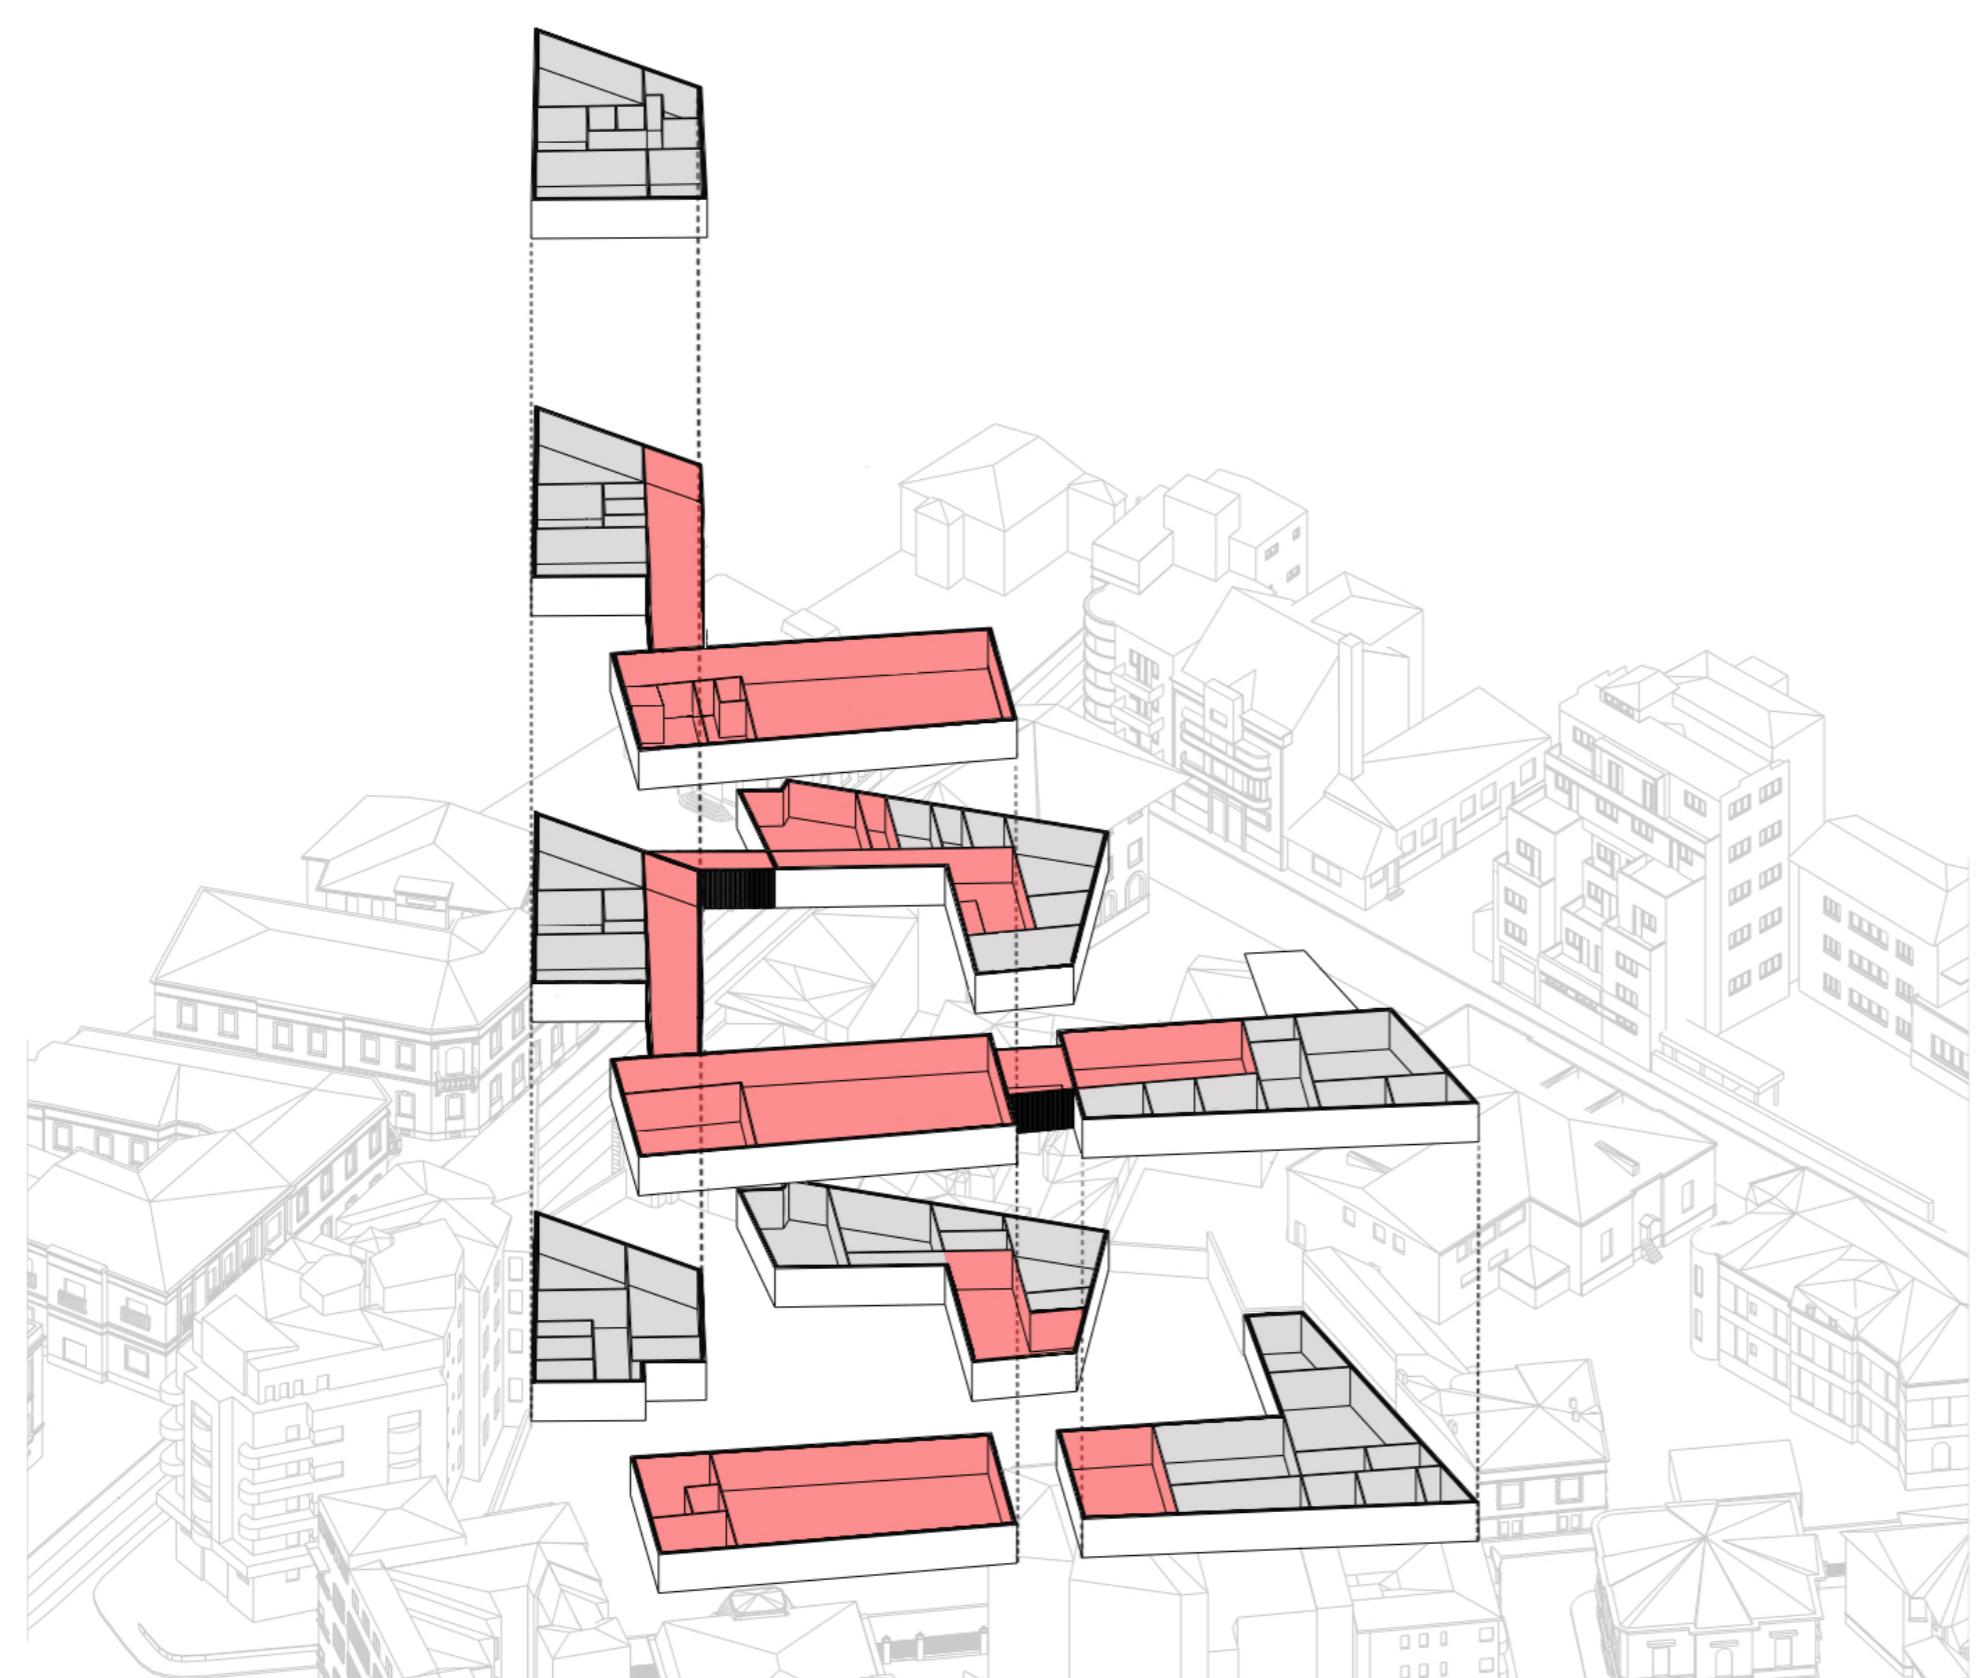


TEMPORALITÉ

Pendant les heures d'école

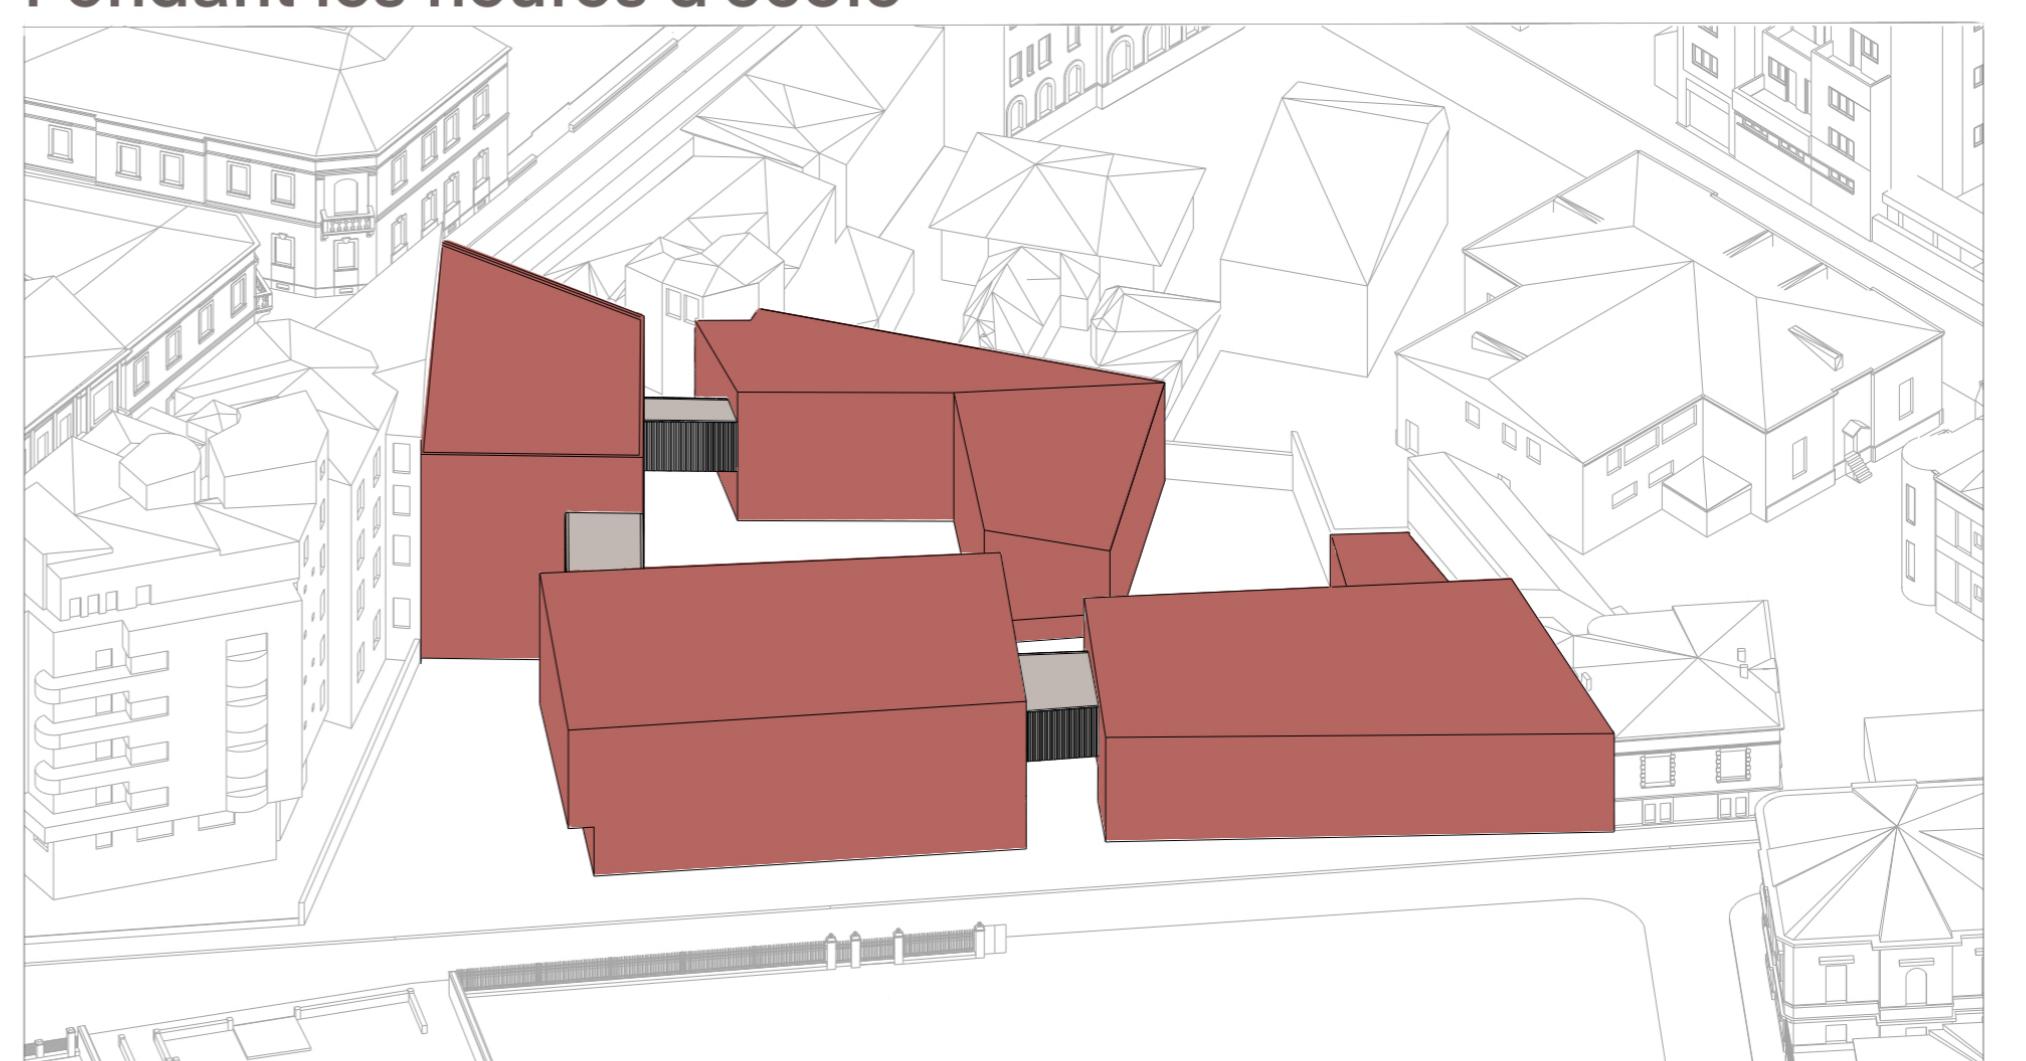

En dehors des heures d'école

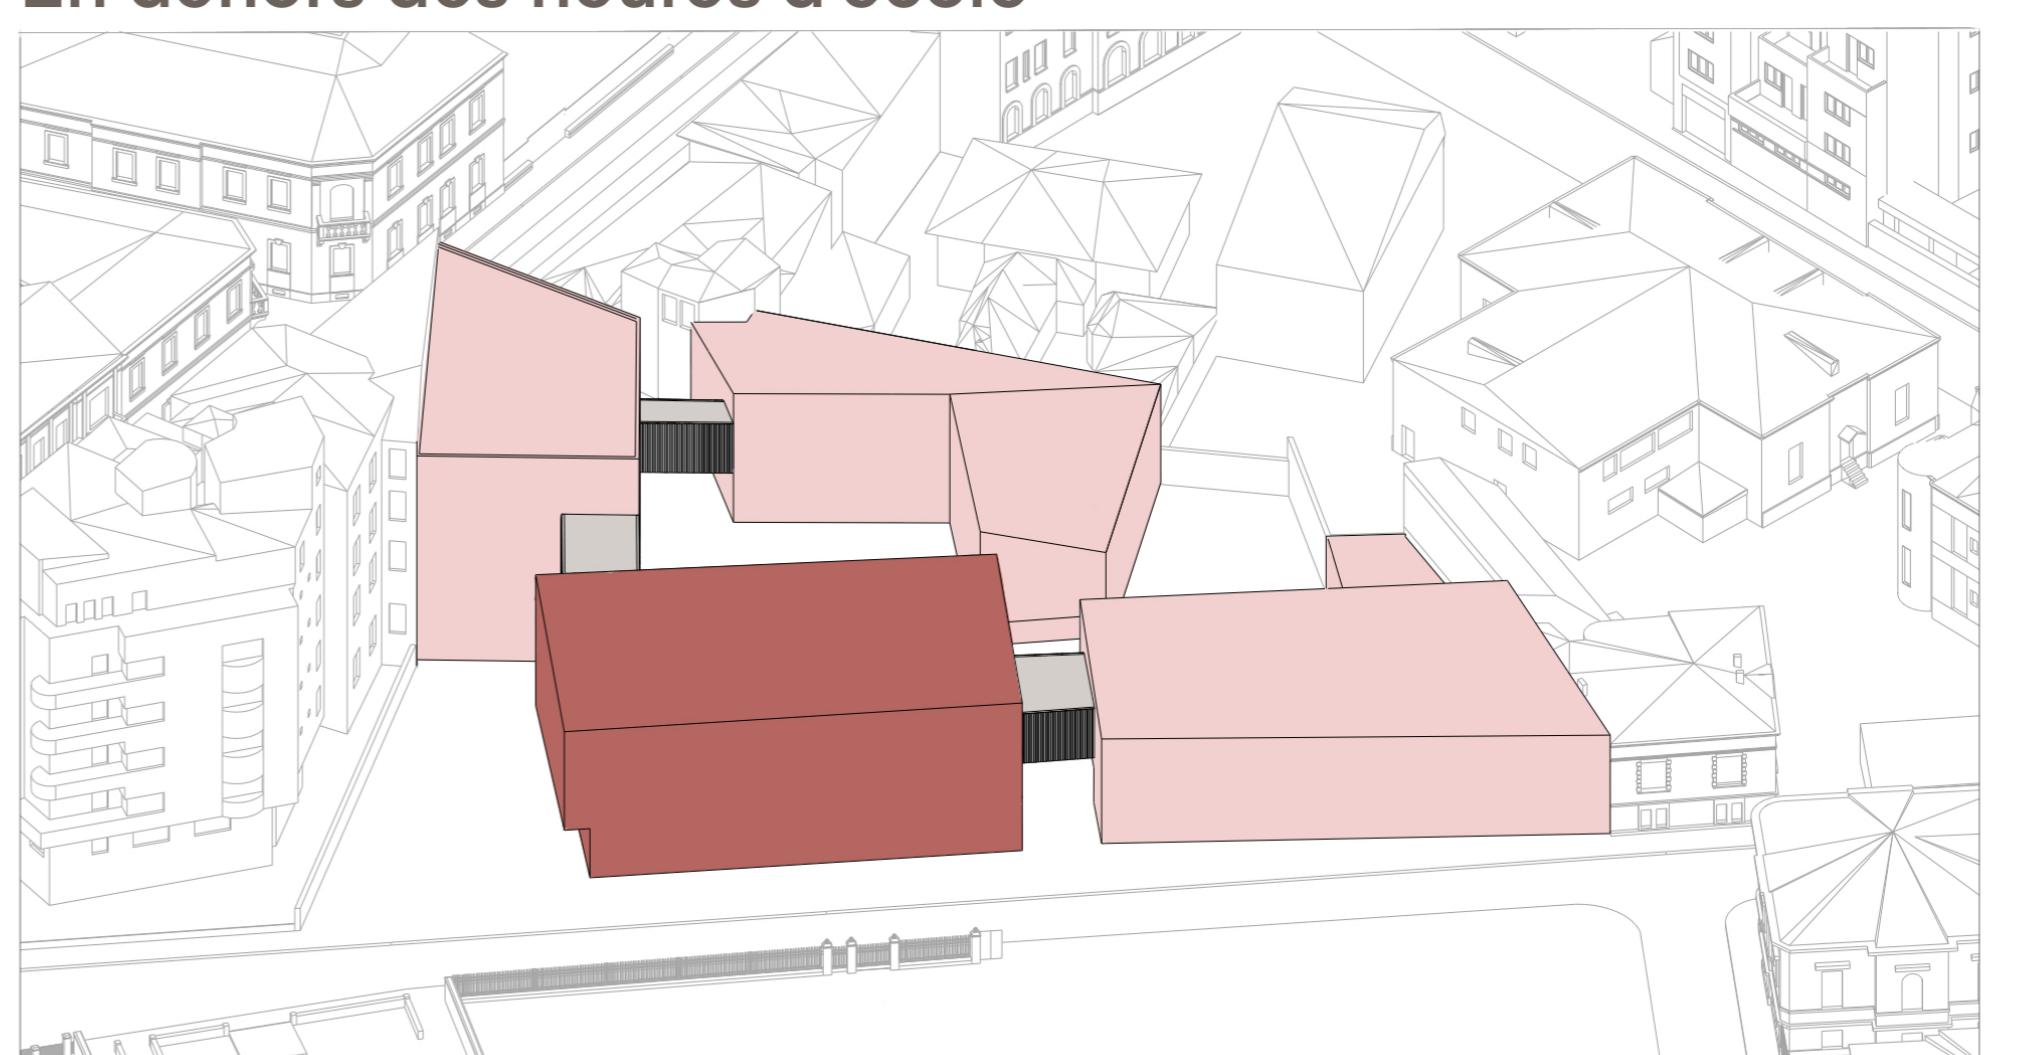

Espaces communs

Espaces privés

Programme utilisé


Programme non utilisé




01 PLAN D'IMPLANTATION
ÉCHELLE : 1/500




ELEVATION EST
ÉCHELLE : 1/200

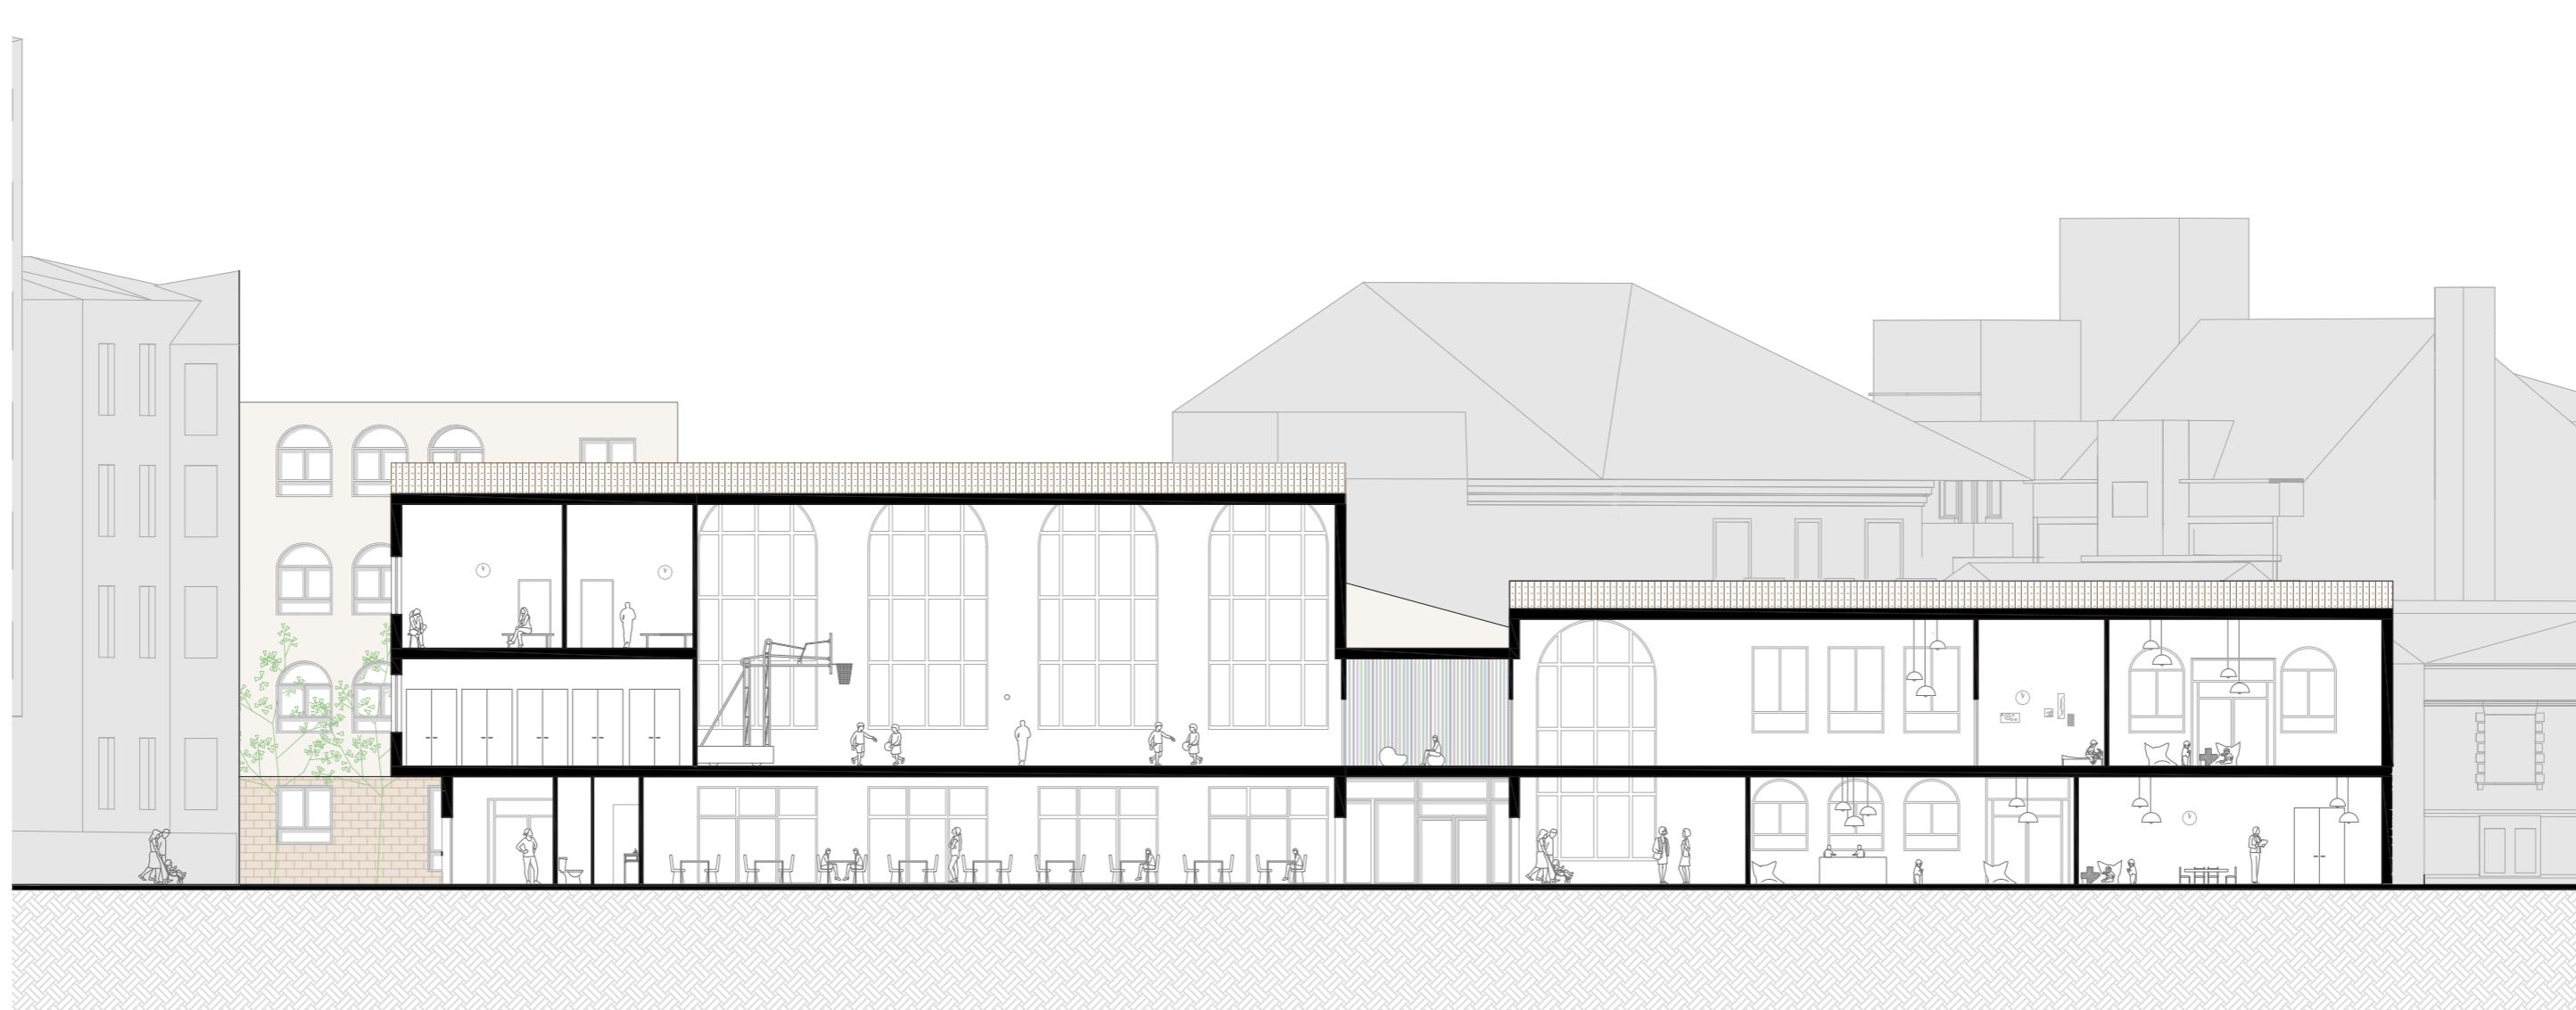


A COUPE AA'
ÉCHELLE : 1/200

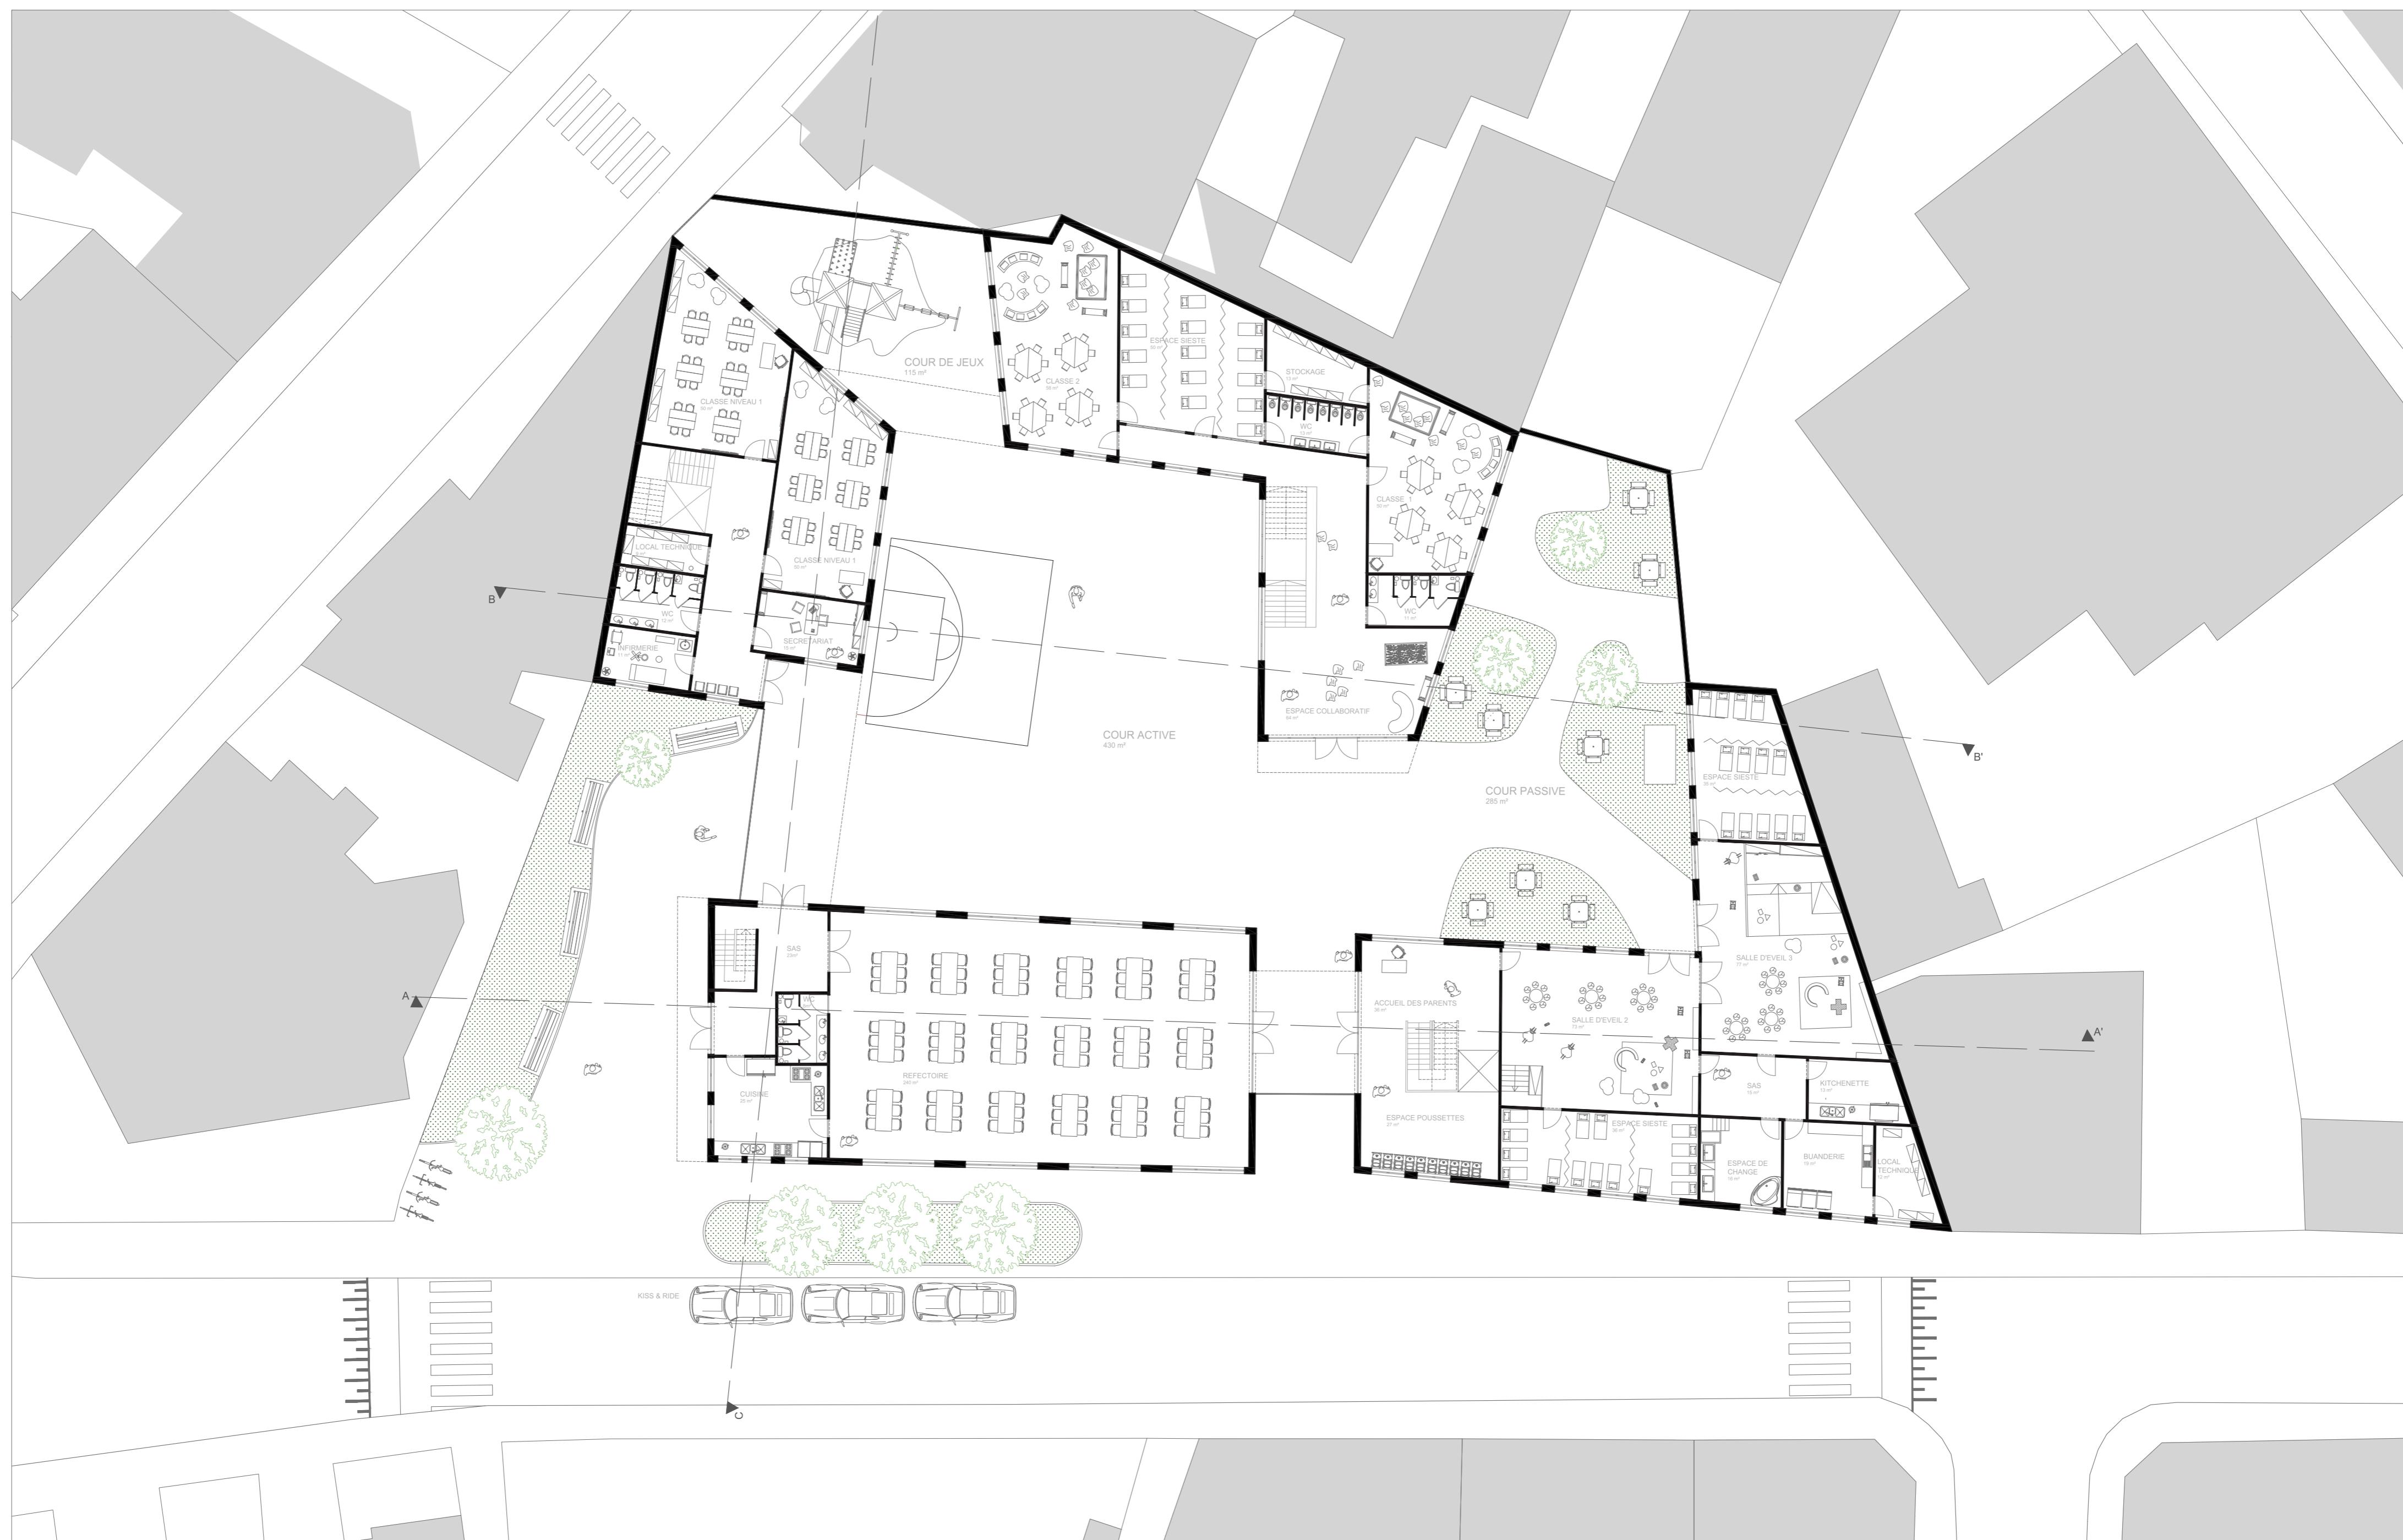


01
04 PLAN DU REZ-DE-CHAUSSEÉ
ÉCHELLE : 1/200

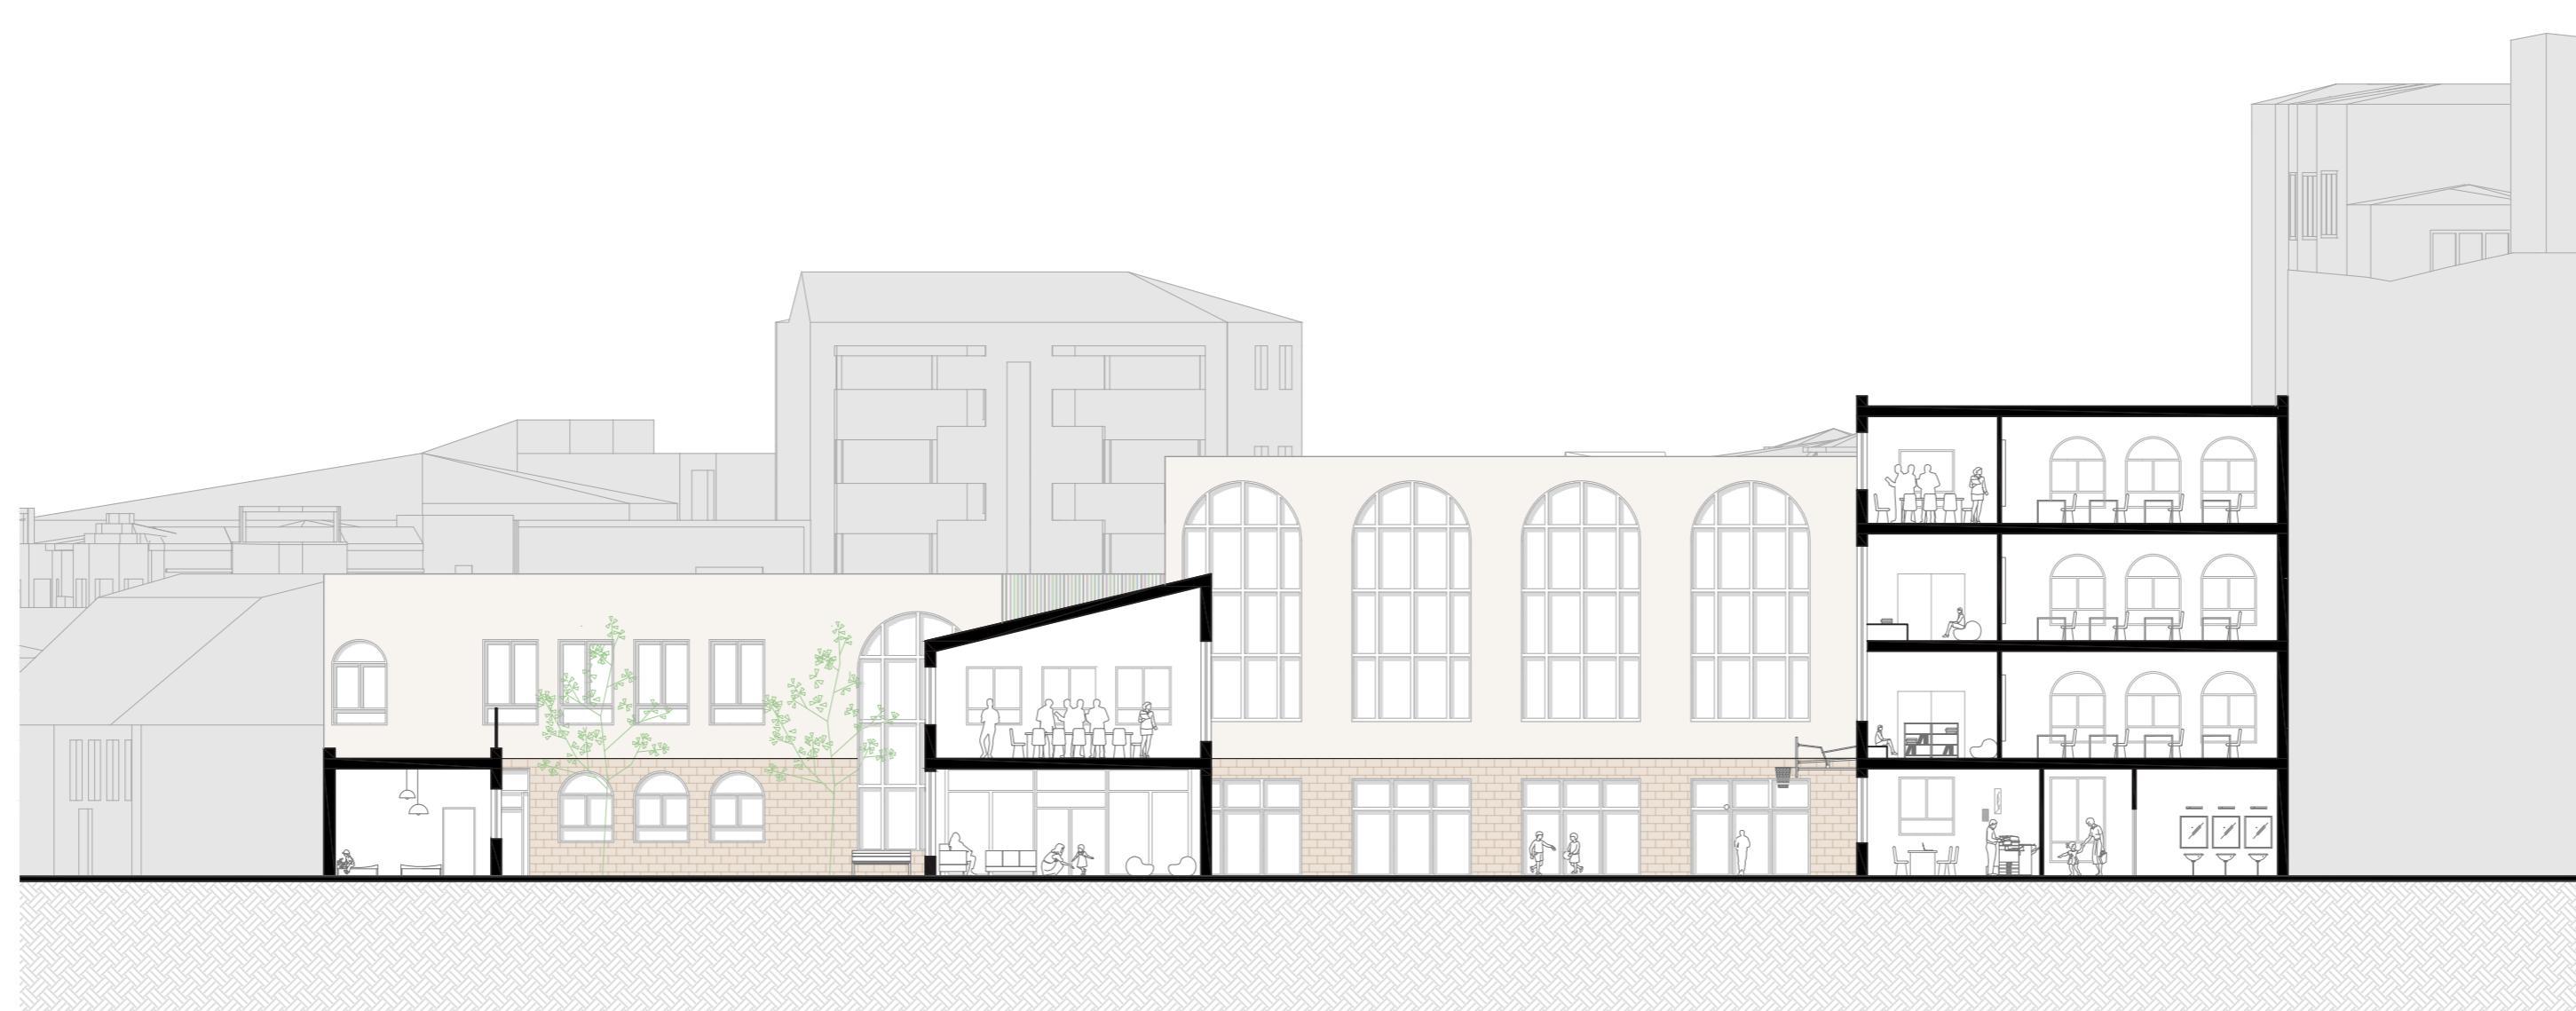


B COUPE BB'
B' ÉCHELLE : 1/200

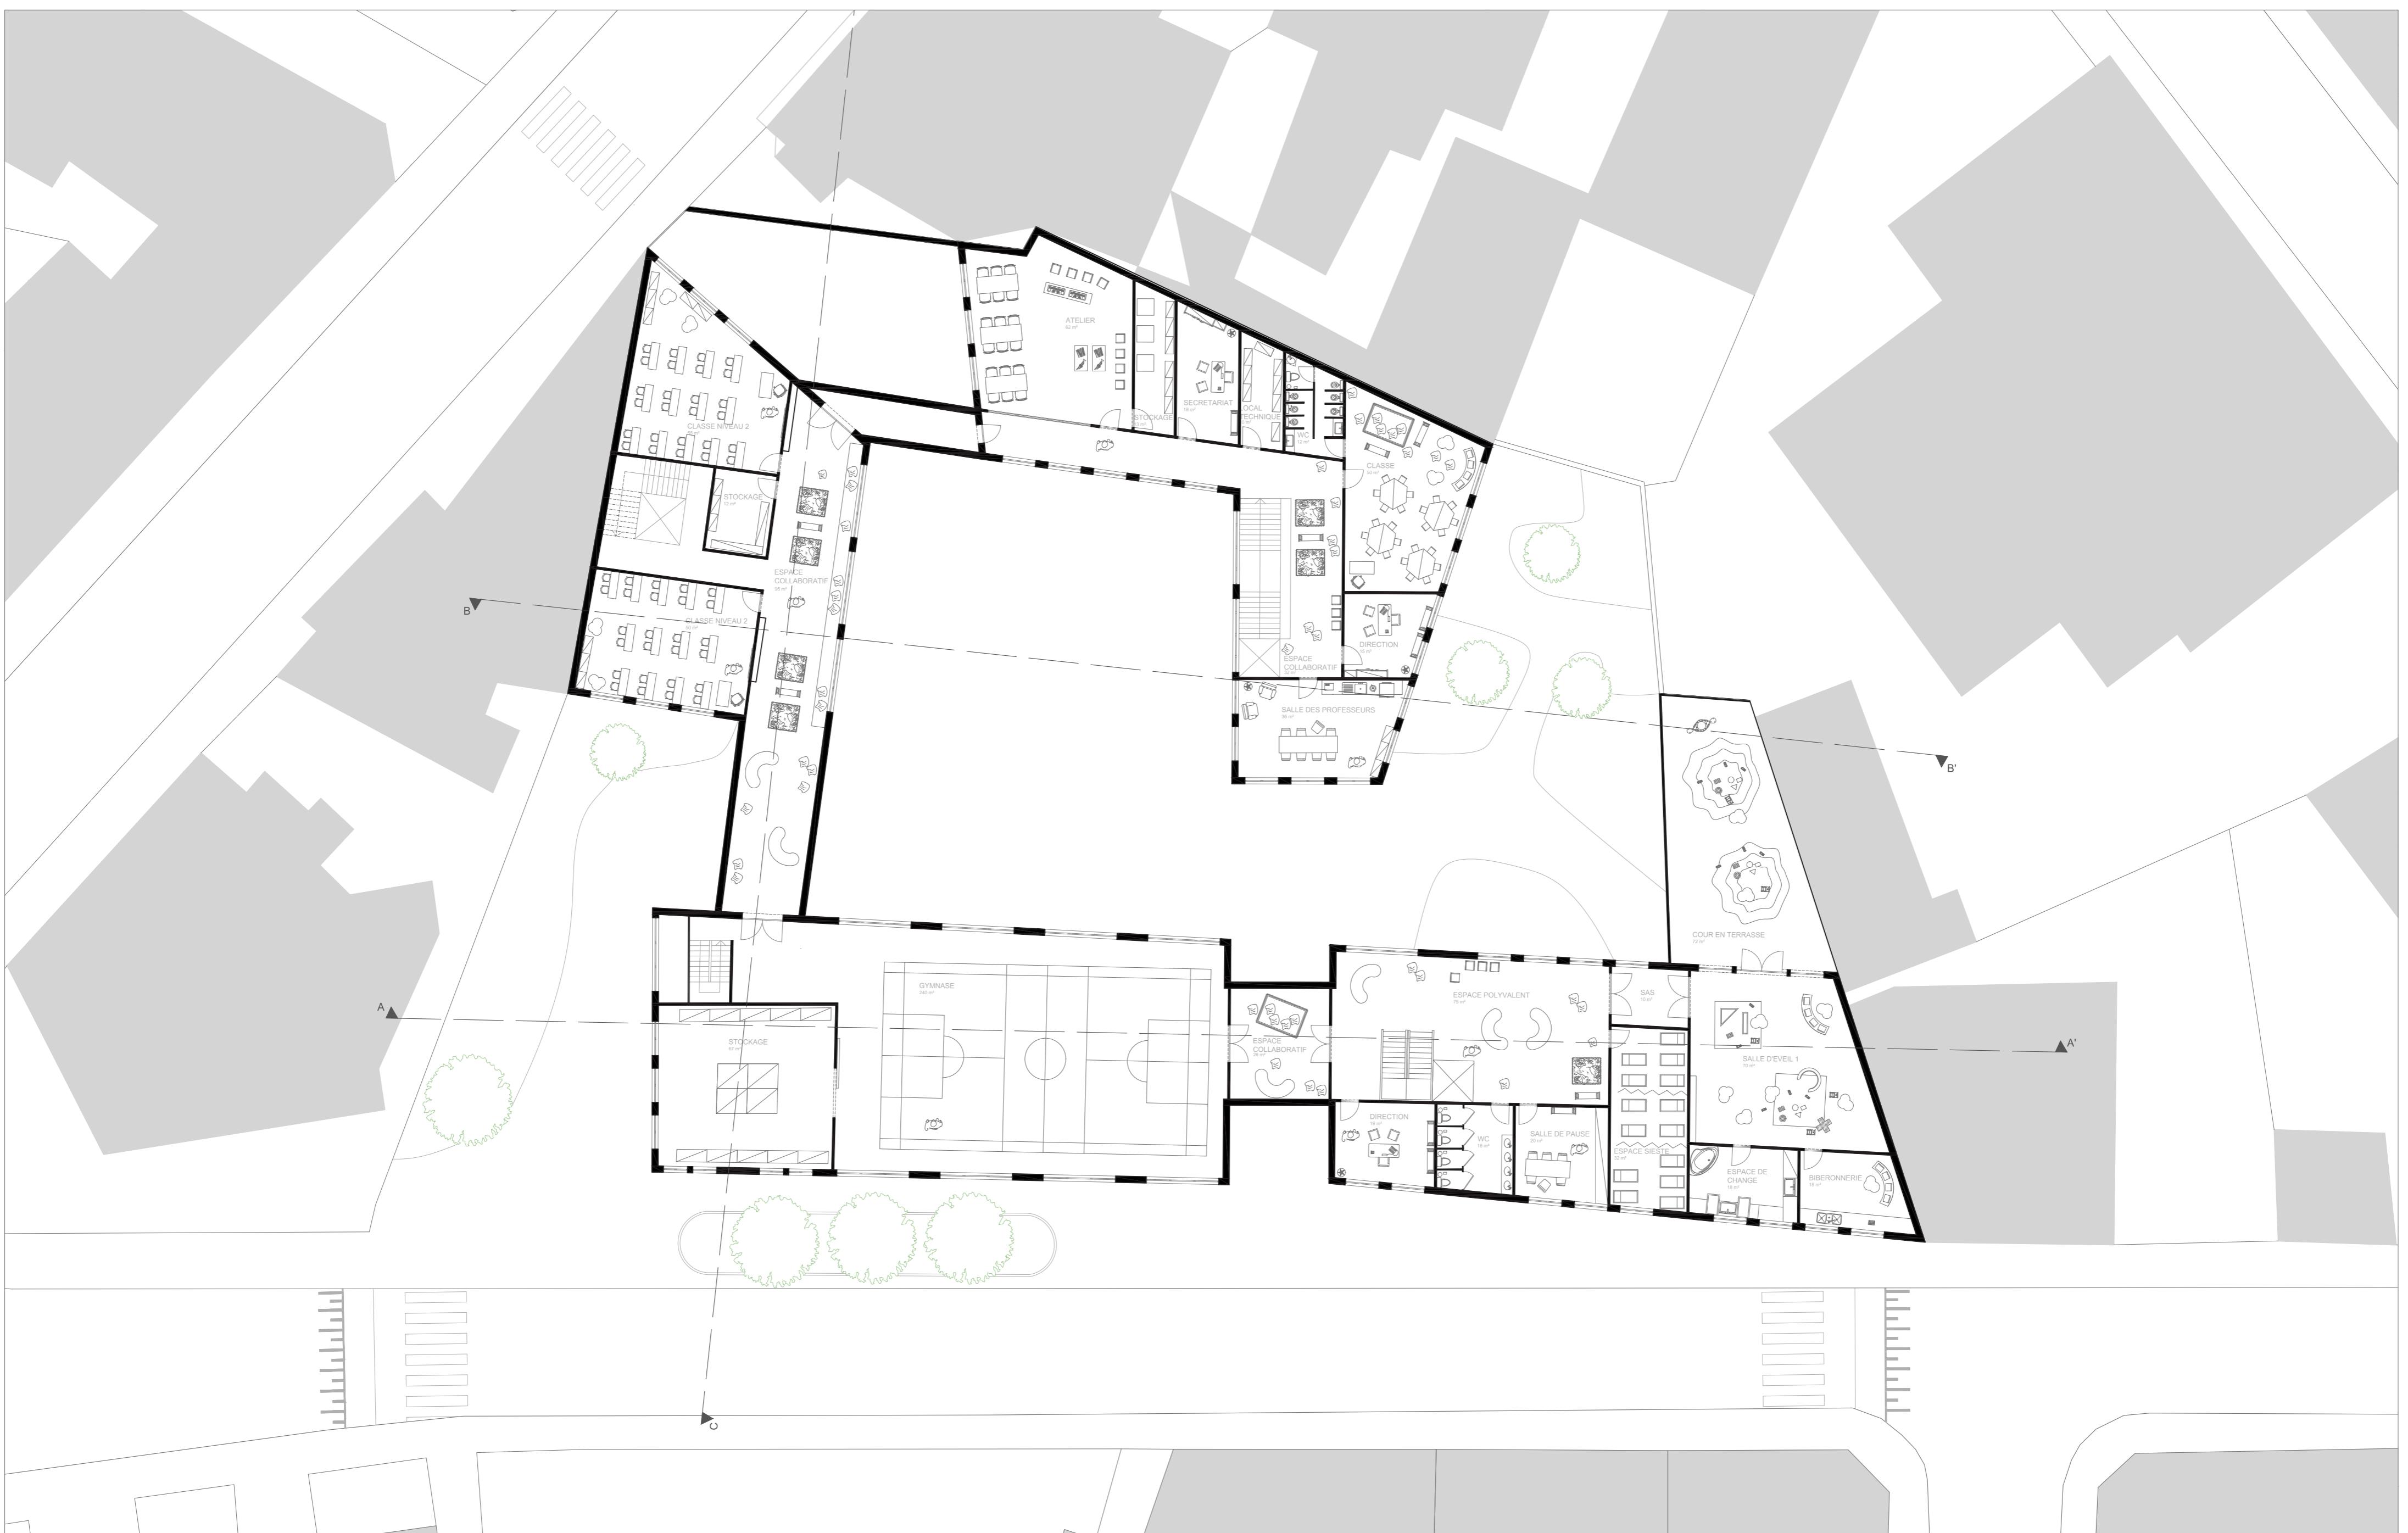

02
04 PLAN DU PREMIER ETAGE
ÉCHELLE : 1/200

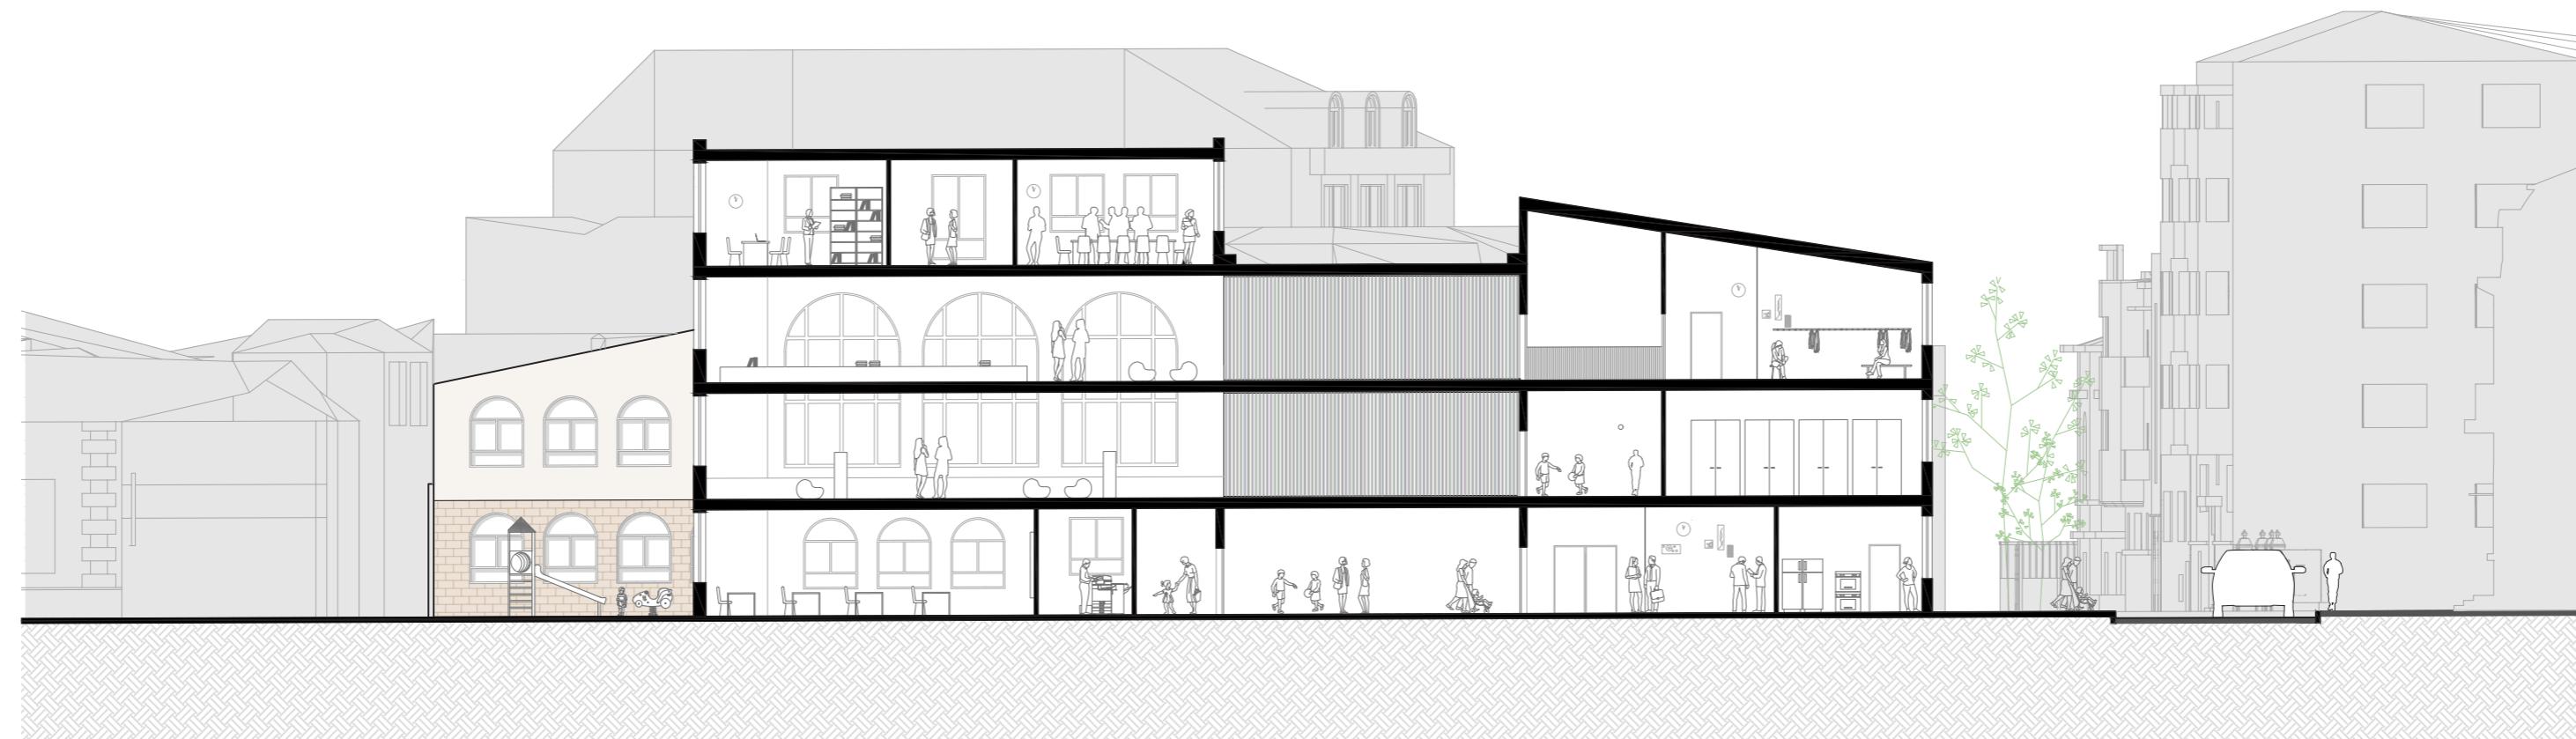

C COUPE CC
C' ÉCHELLE : 1/200

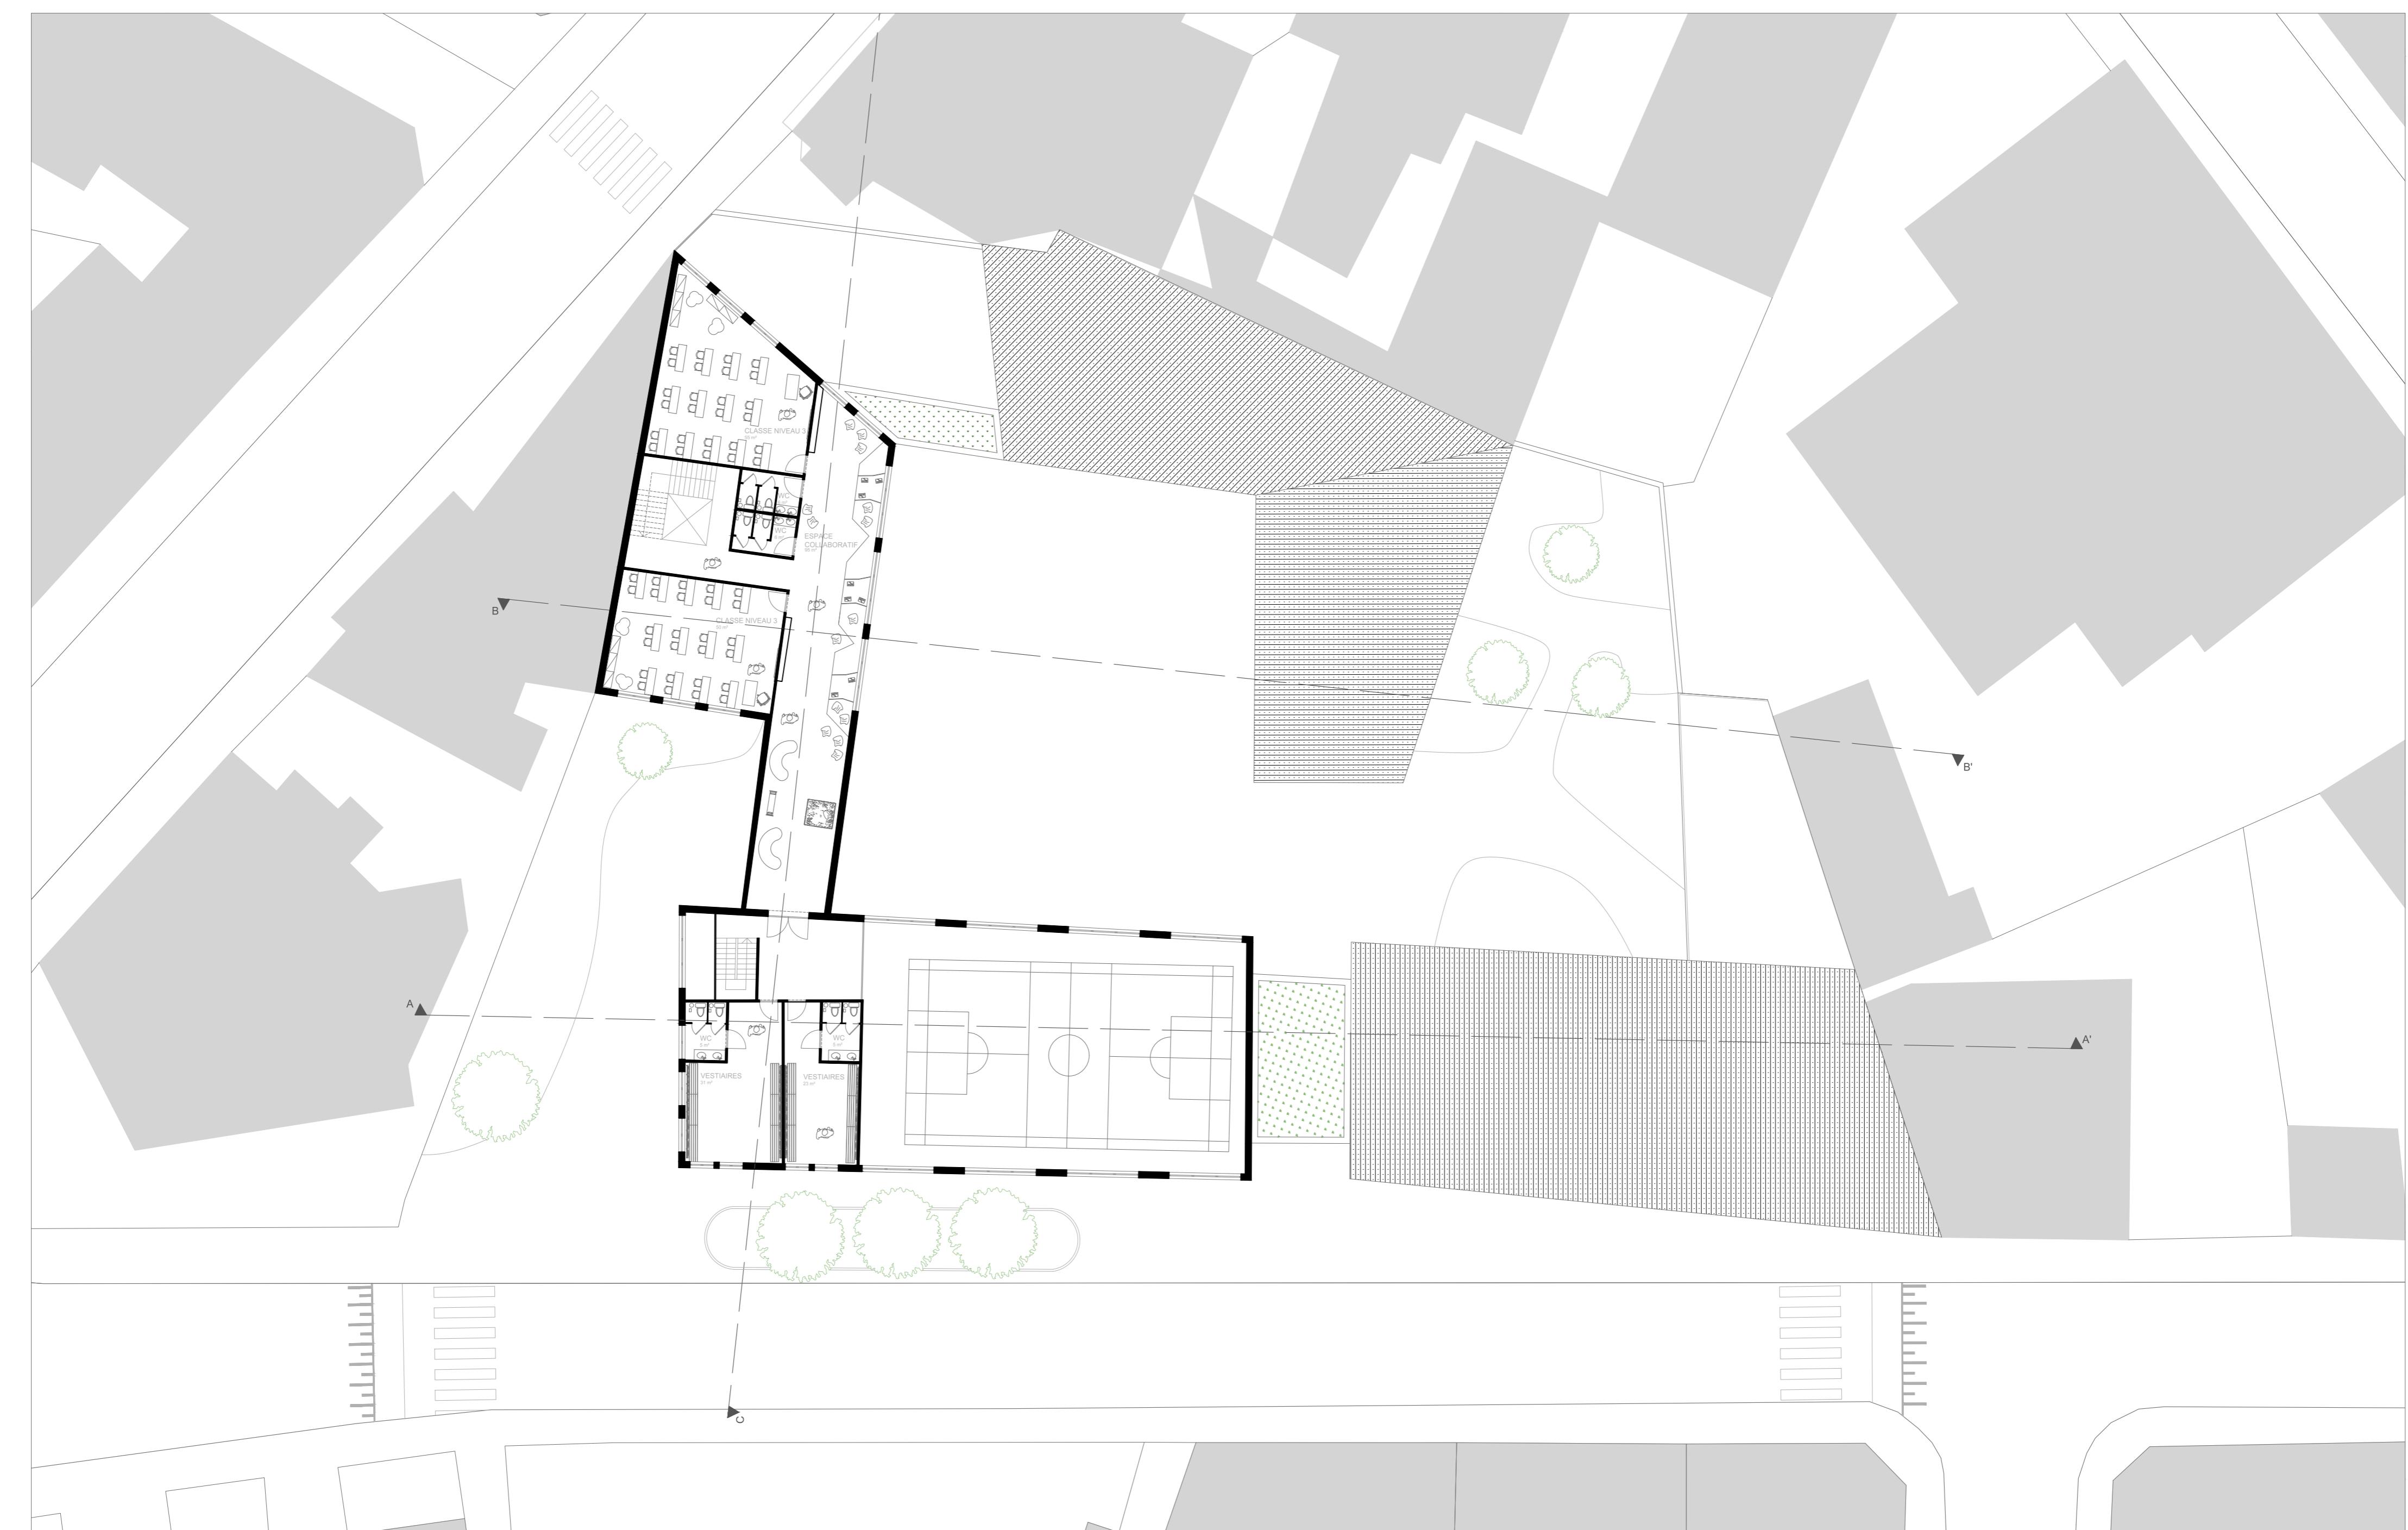

 03 PLAN DU DEUXIEME ETAGE
04 ÉCHELLE : 1/200



